


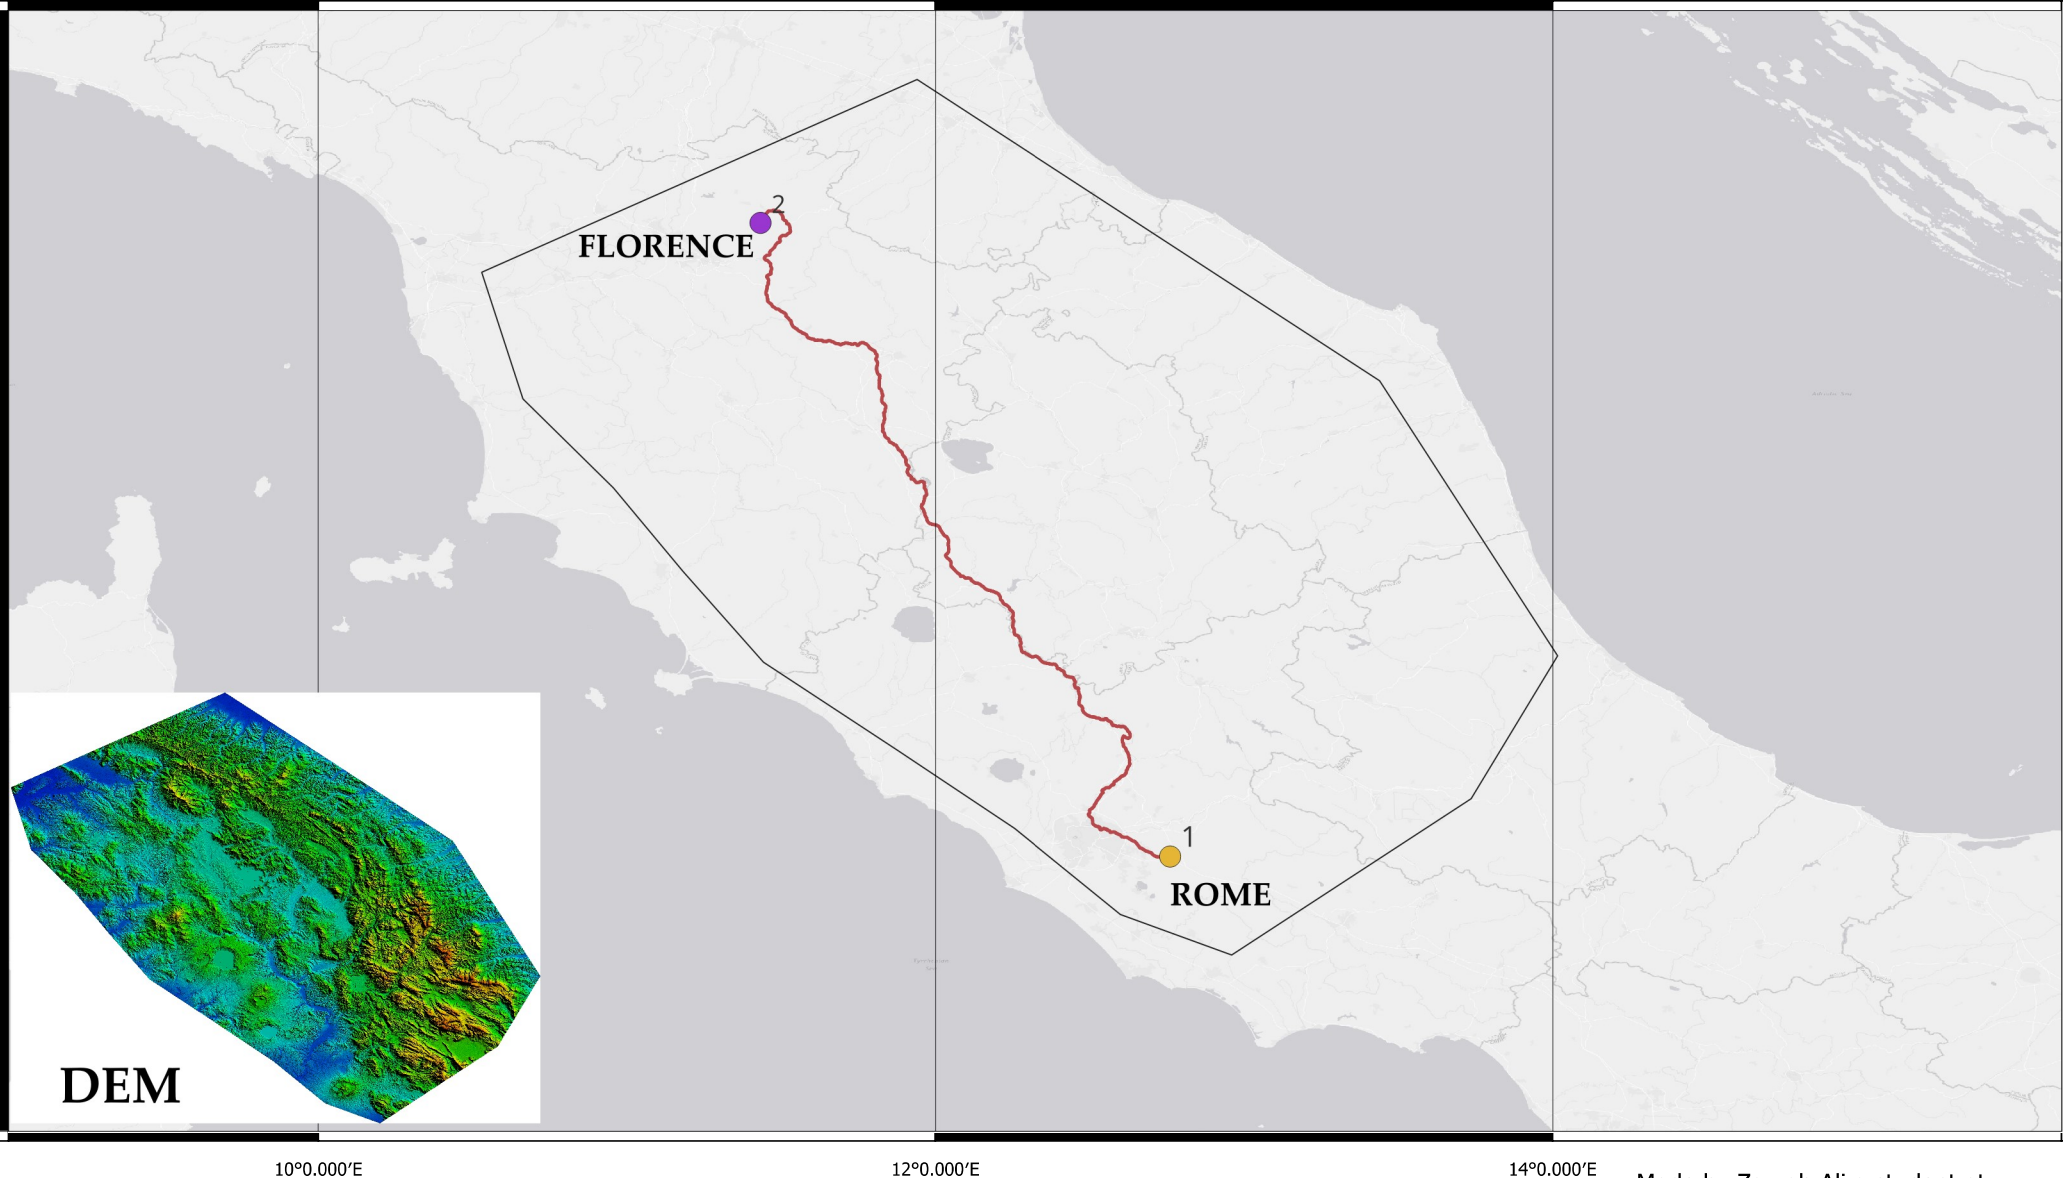

10°0.000'E


12°0.000'E

14°0.000'E




Made by Zaryab Ali, a student at
NED-UET



Highway route design from Rome to Florence optimized for cost-efficiency, minimal slope, reduced cut and fill, and adherence to existing routes where possible. The design leverages SRTM DEM data to ensure the most feasible alignment, considering both environmental and engineering factors. Project coordinates are referenced in WGS84 EPSG:4326 CRS for accuracy and consistency.

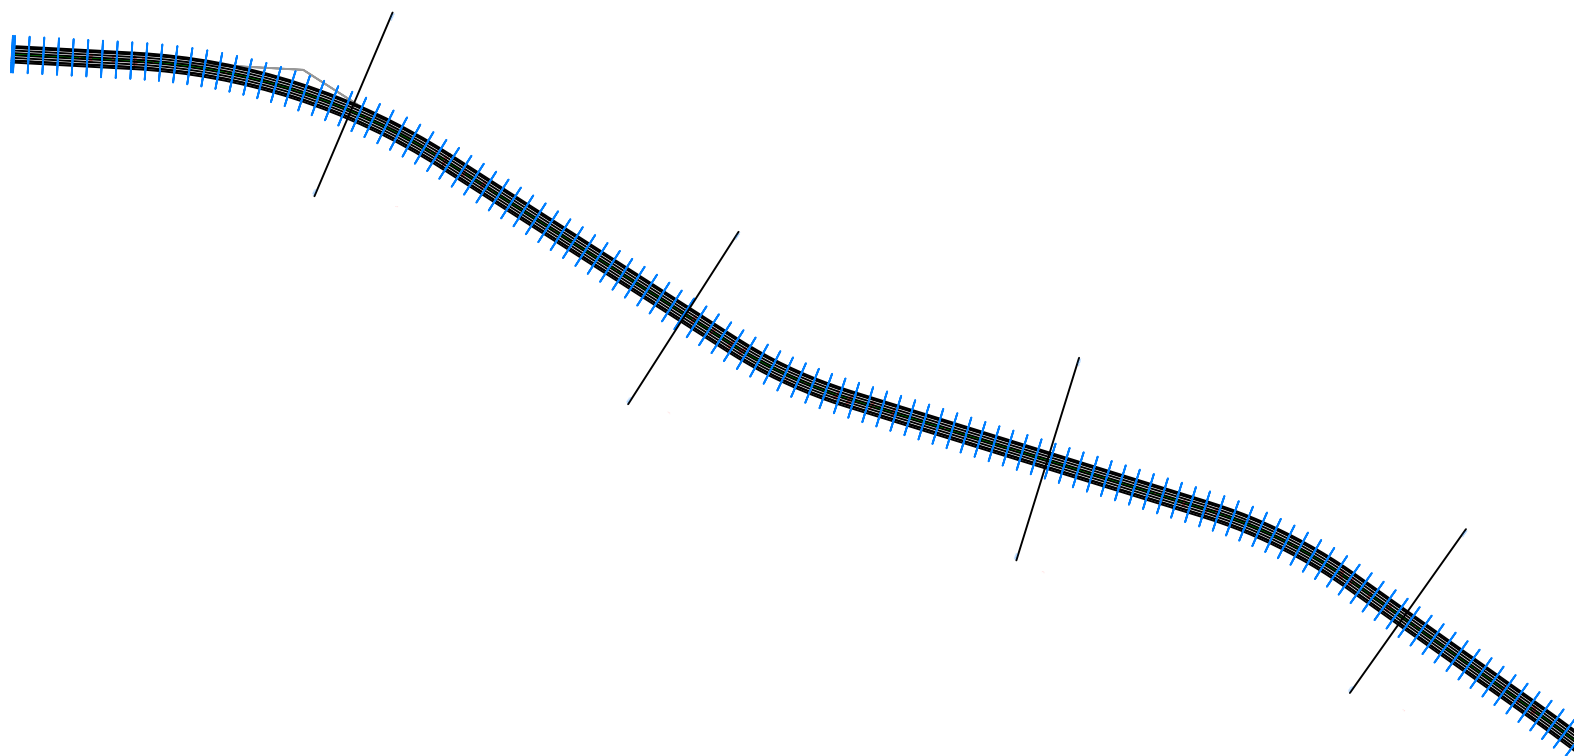

Road Design Profile

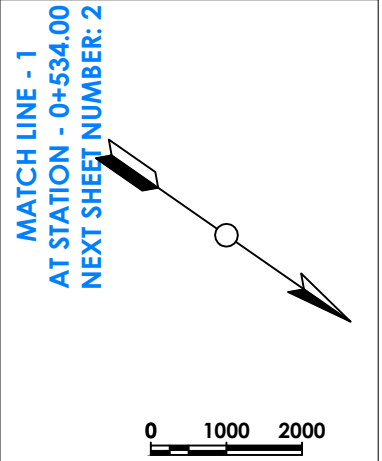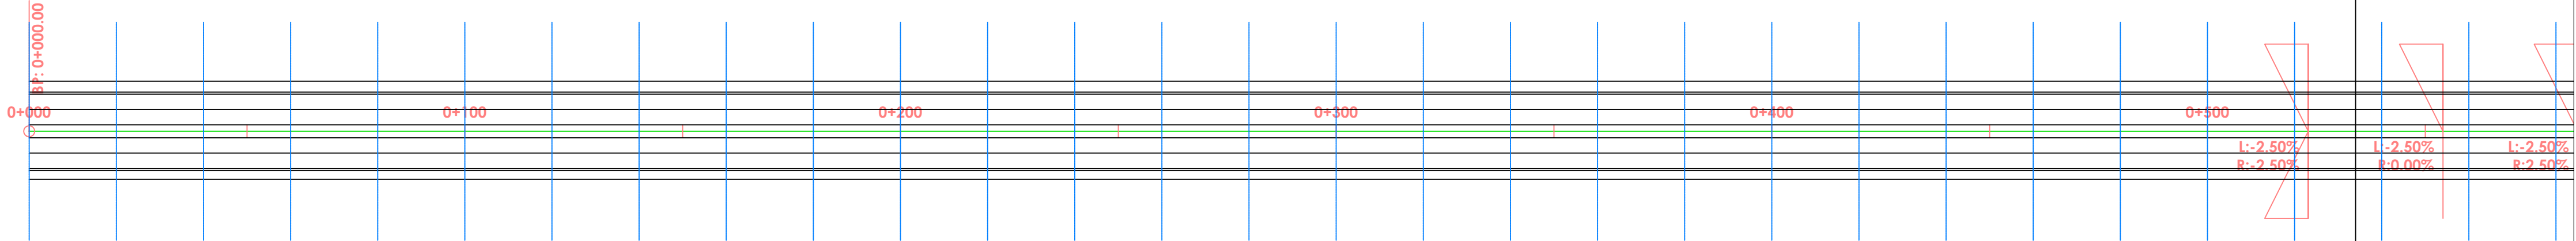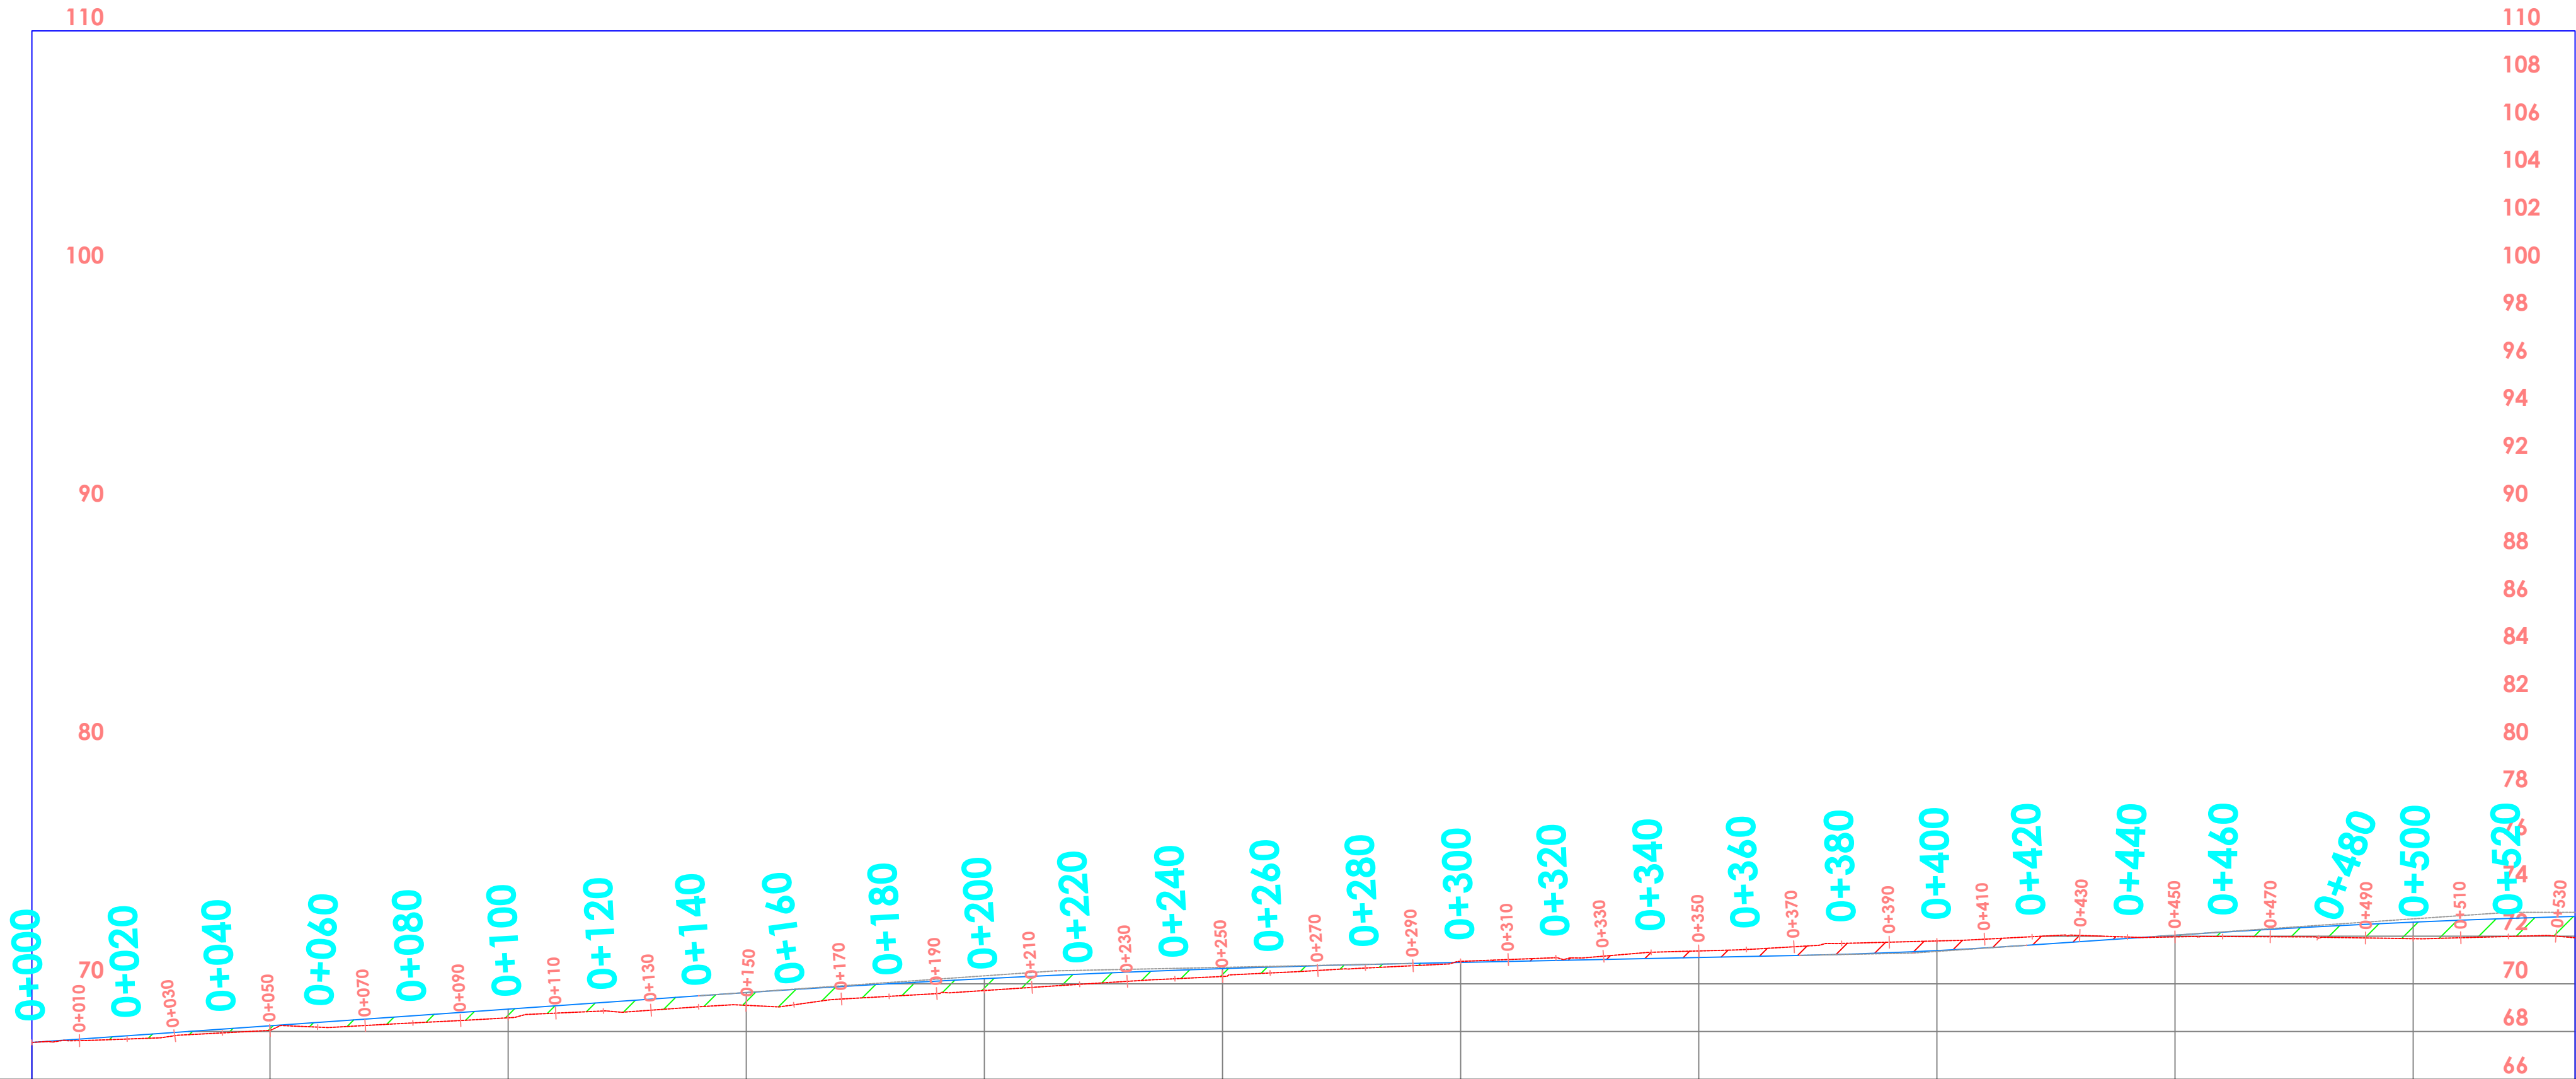

MATCH LINE - 1
AT STATION - 0+534.00
NEXT SHEET NUMBER: 2

General Notes

No.	Revision/Issue	Date
-----	----------------	------

Firm Name and Address


Project Name and Address

Project
#####

Date
03.04.2025

Scale
1:1000

Sheet
1

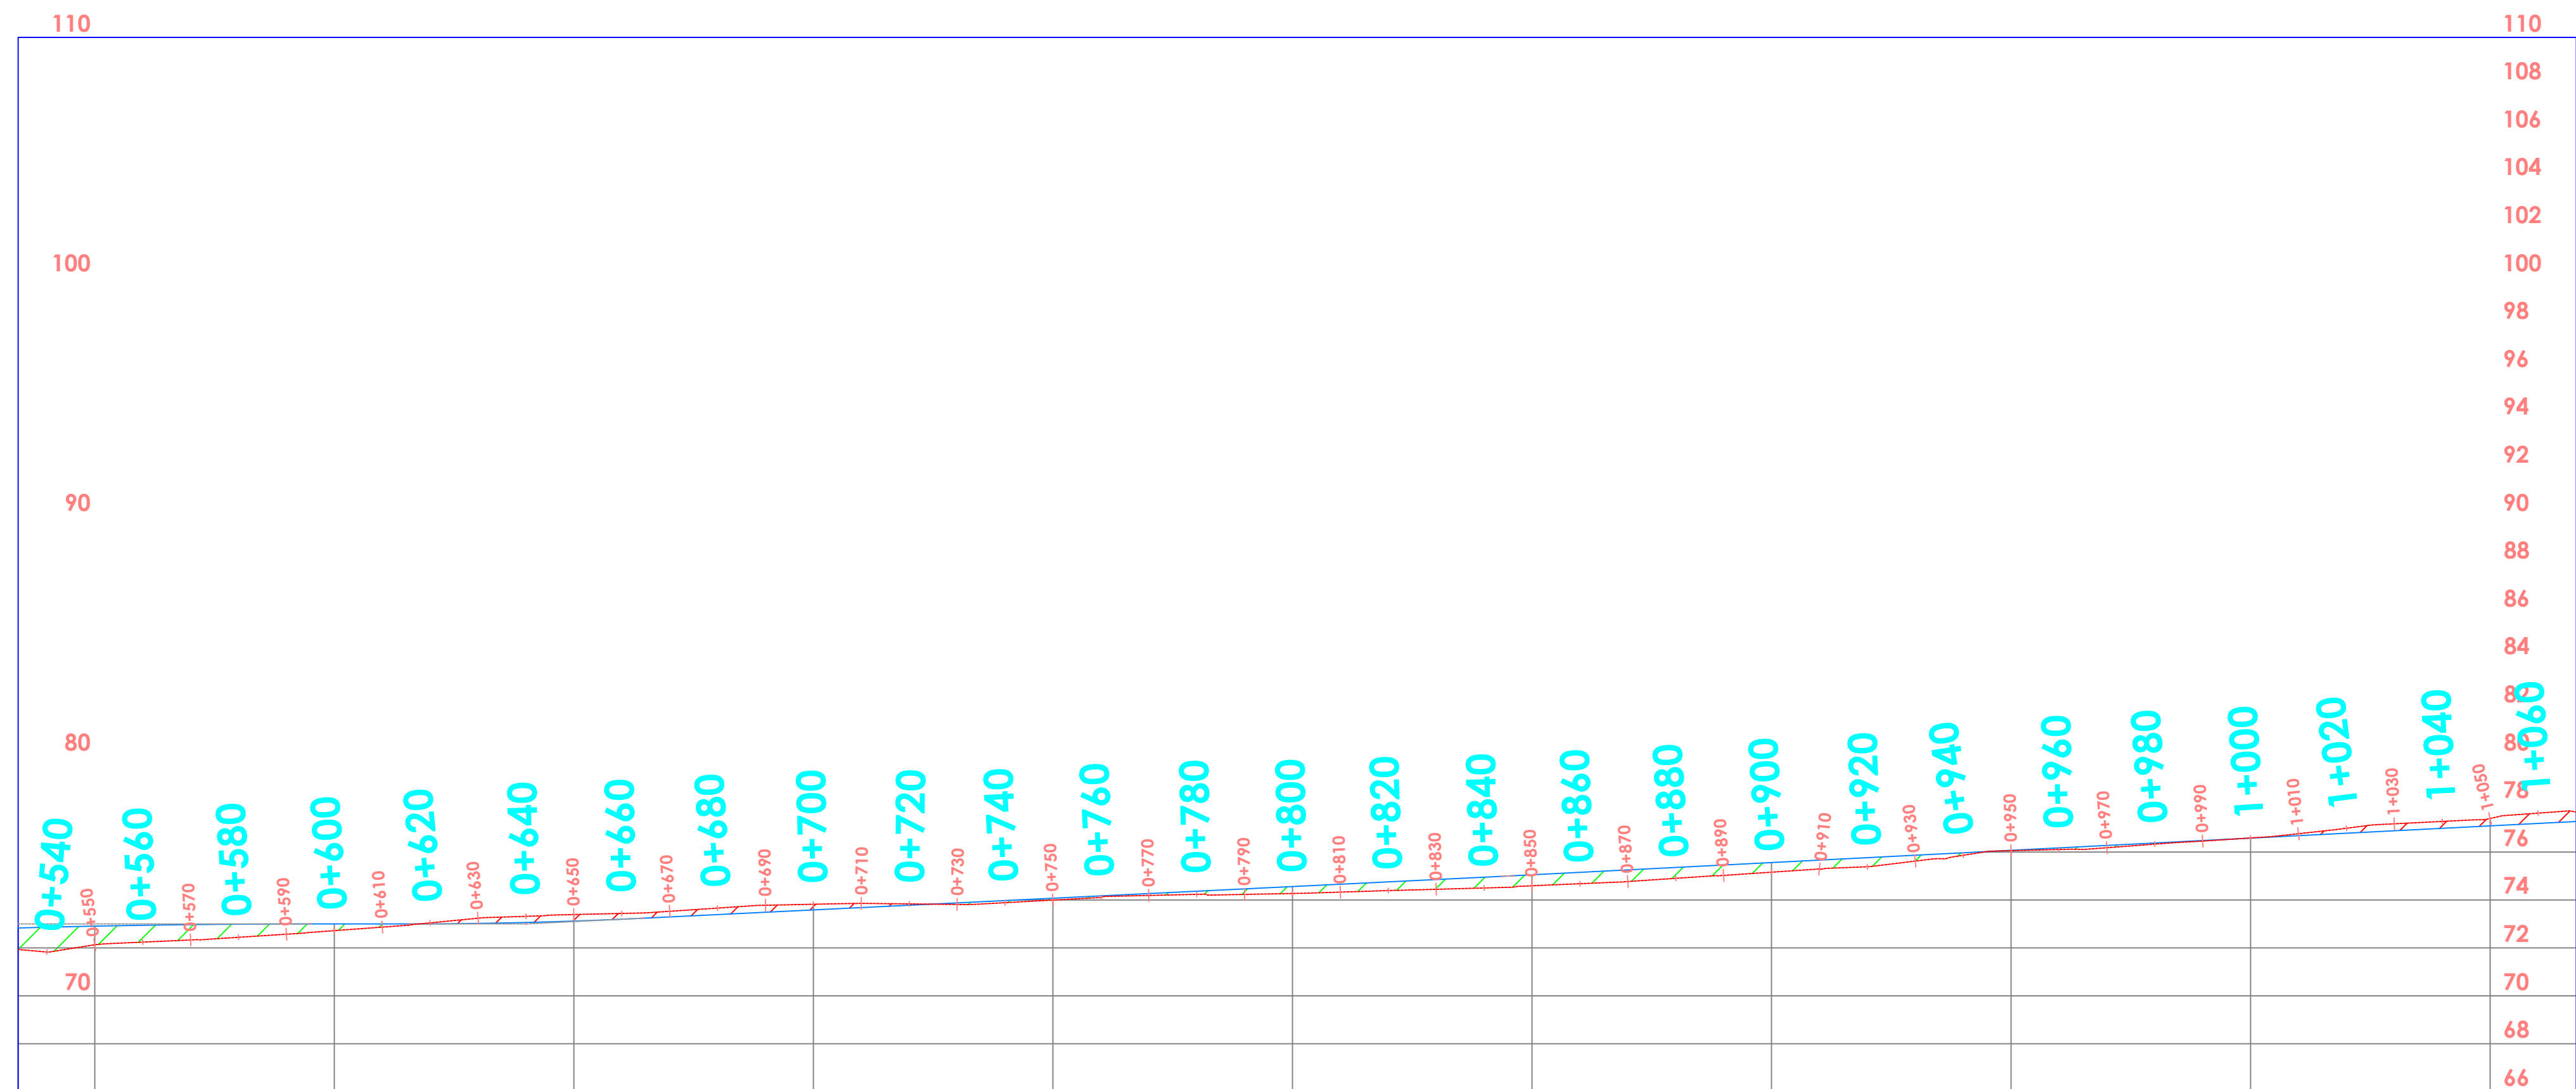

No.	Revision/Issue	Date
-----	----------------	------

Firm Name and Address

Project Name and Address

#####


Project # # # # #

Date
03.04.2025


Scale
1:1000

heet

2

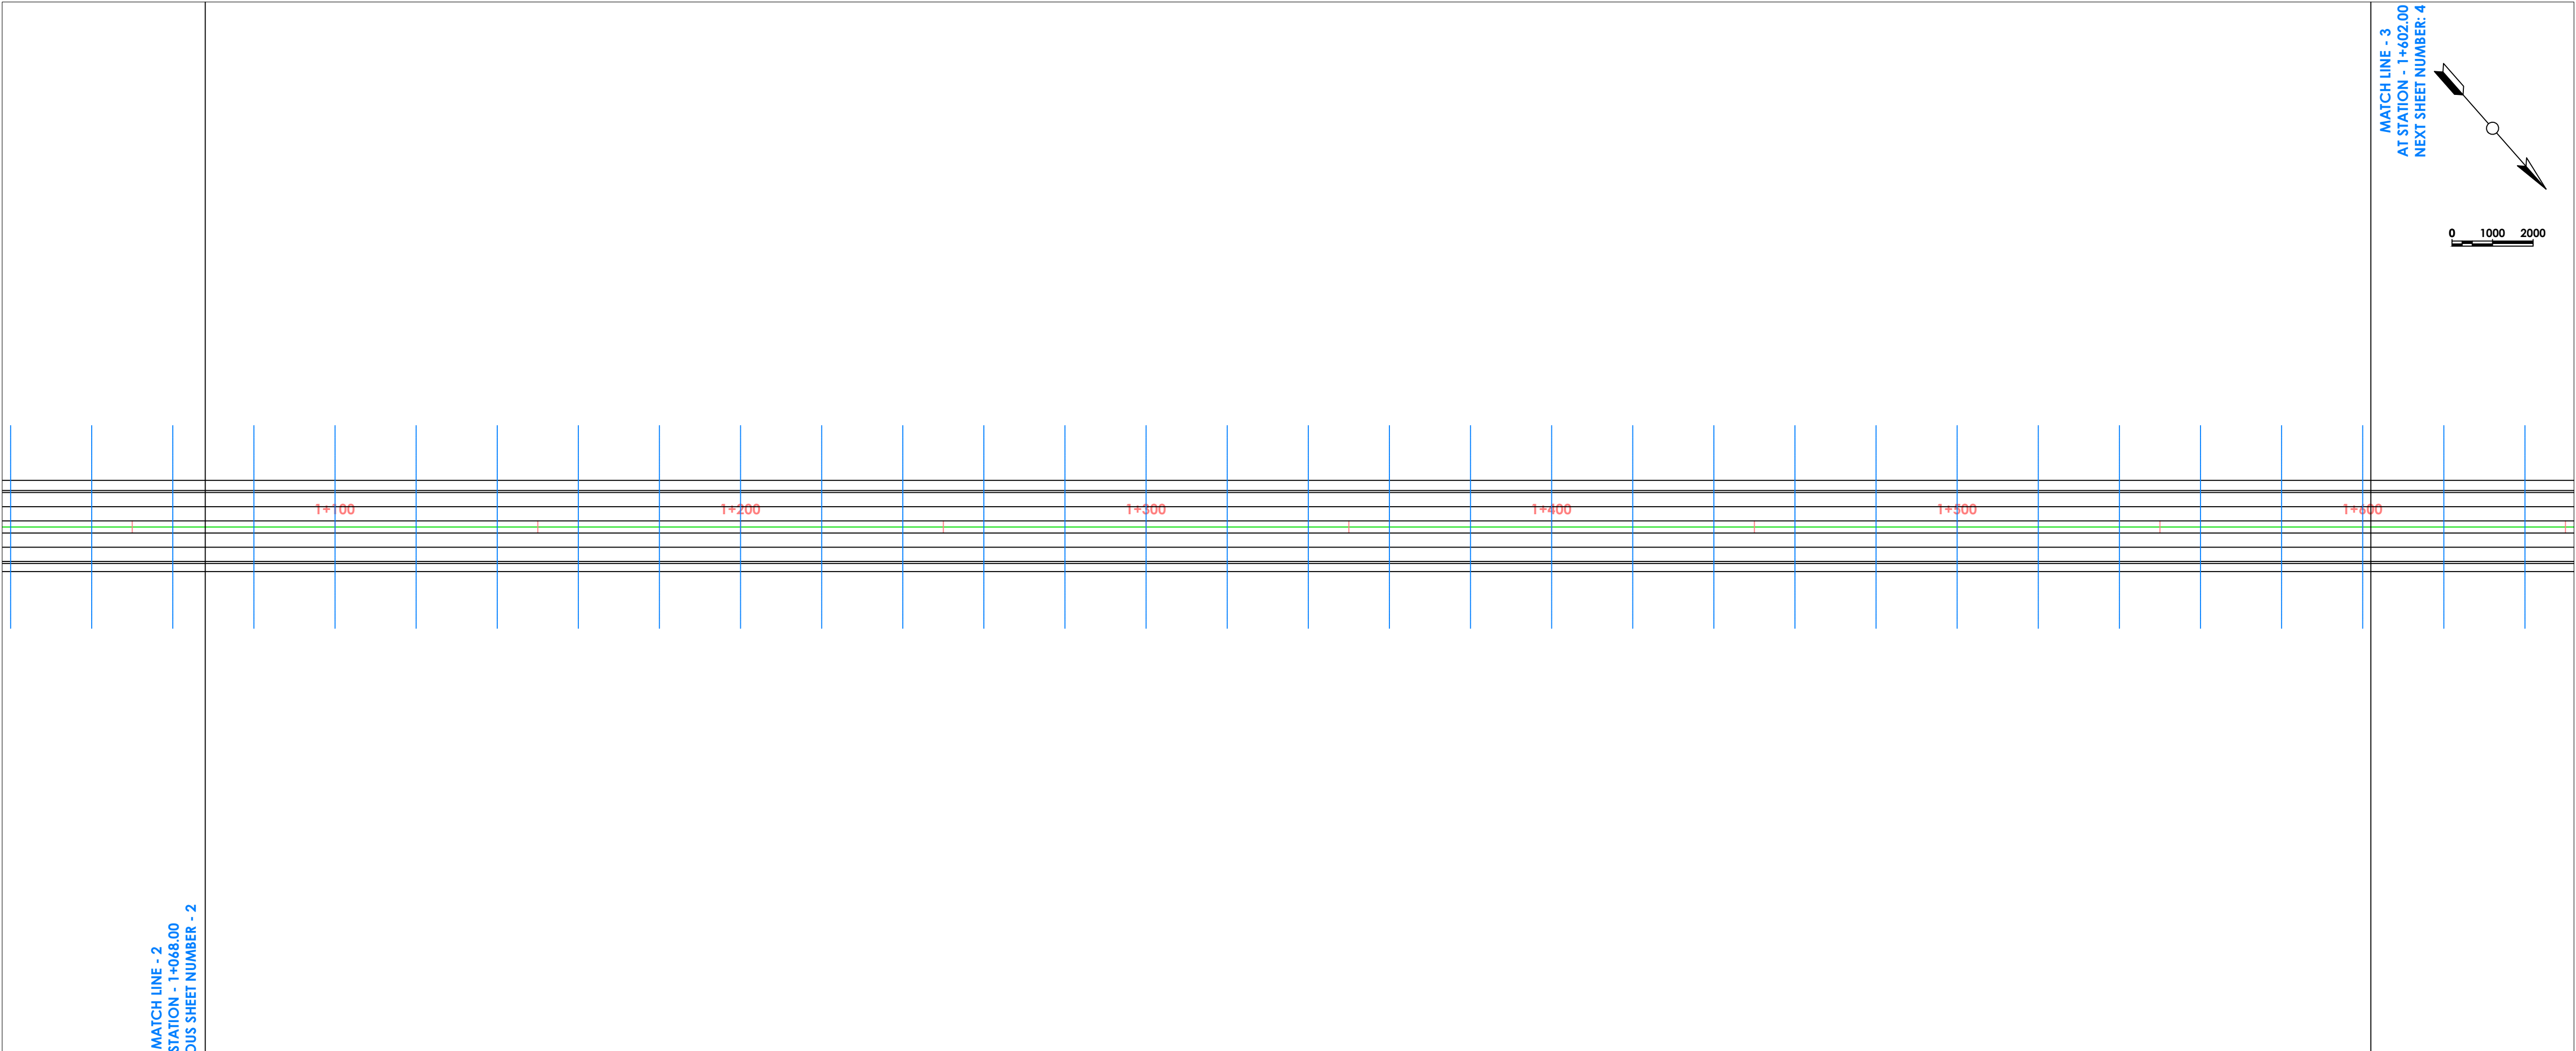

Road Design Profile

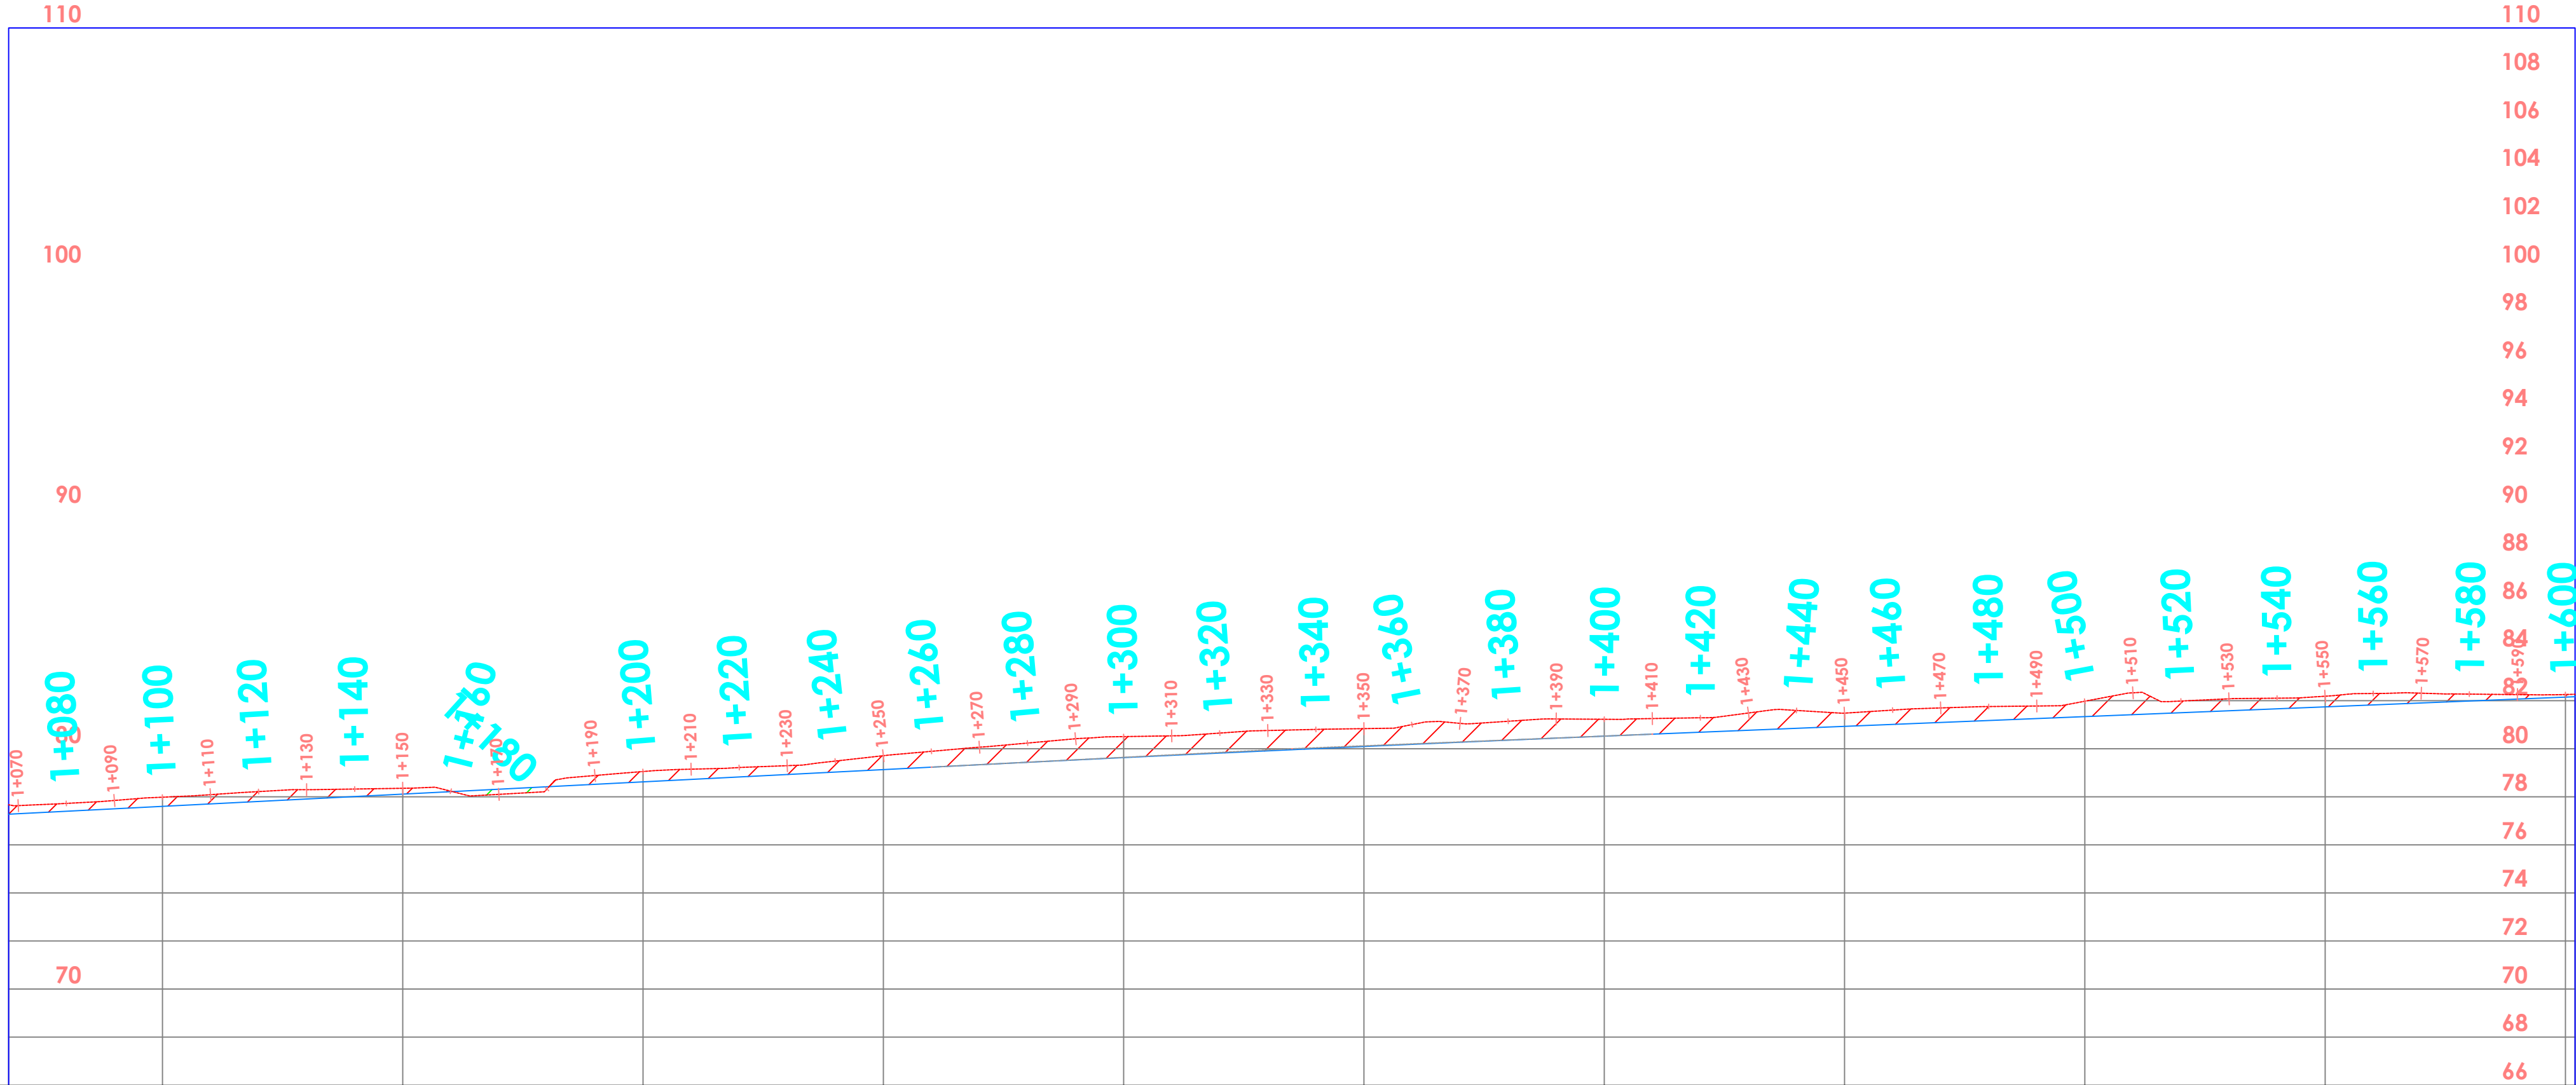

General Notes

No.	Revision/Issue	Date
-----	----------------	------

Firm Name and Address

Project Name and Address

Project

####

Date


03.04.2025

Scale


1:1000

Sheet

3

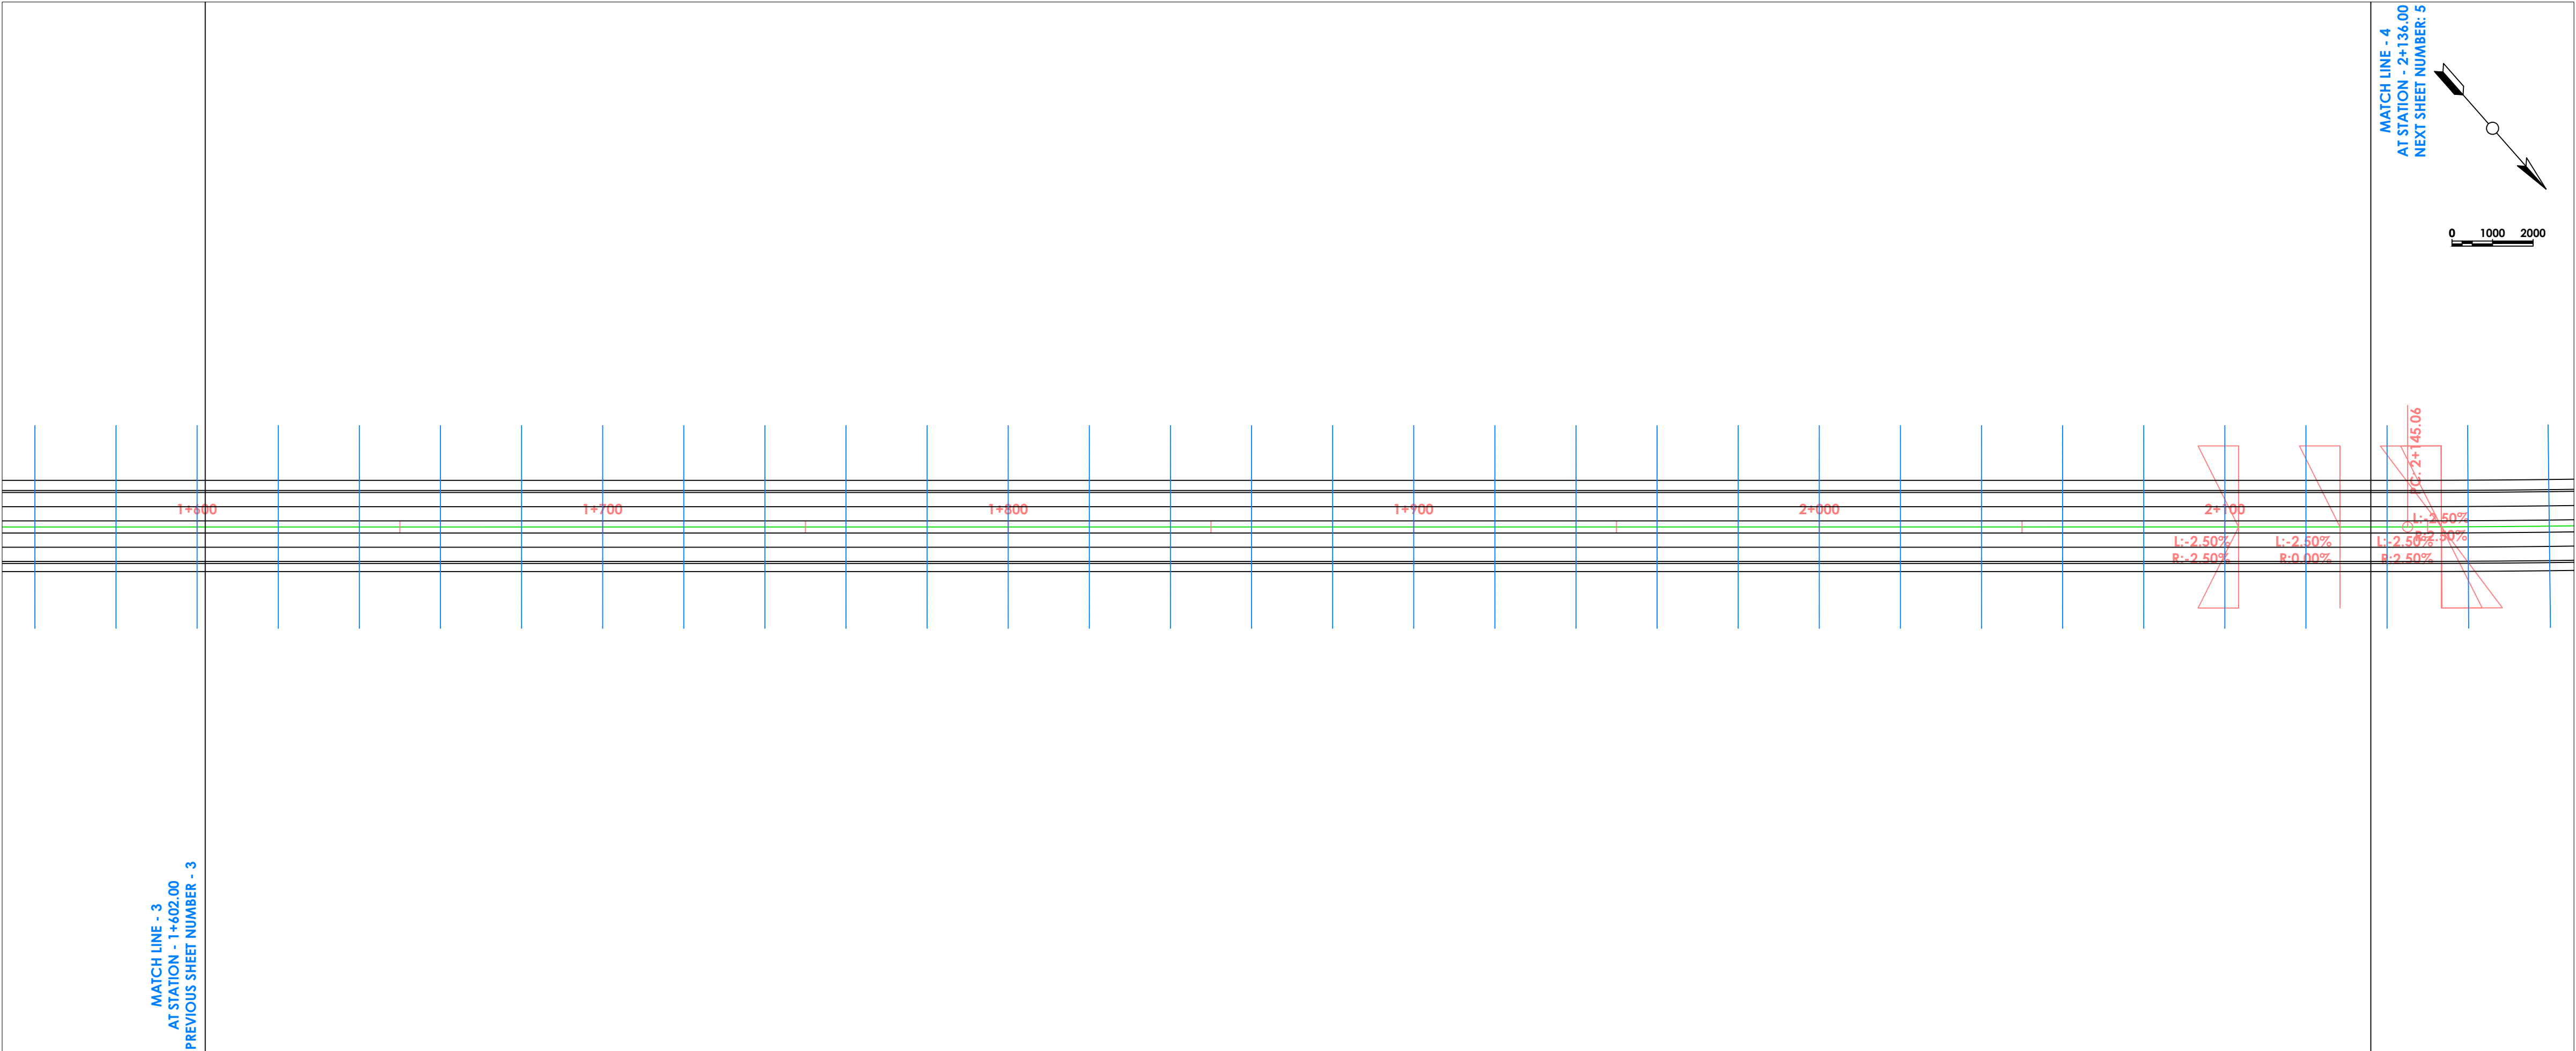

Road Design Profile

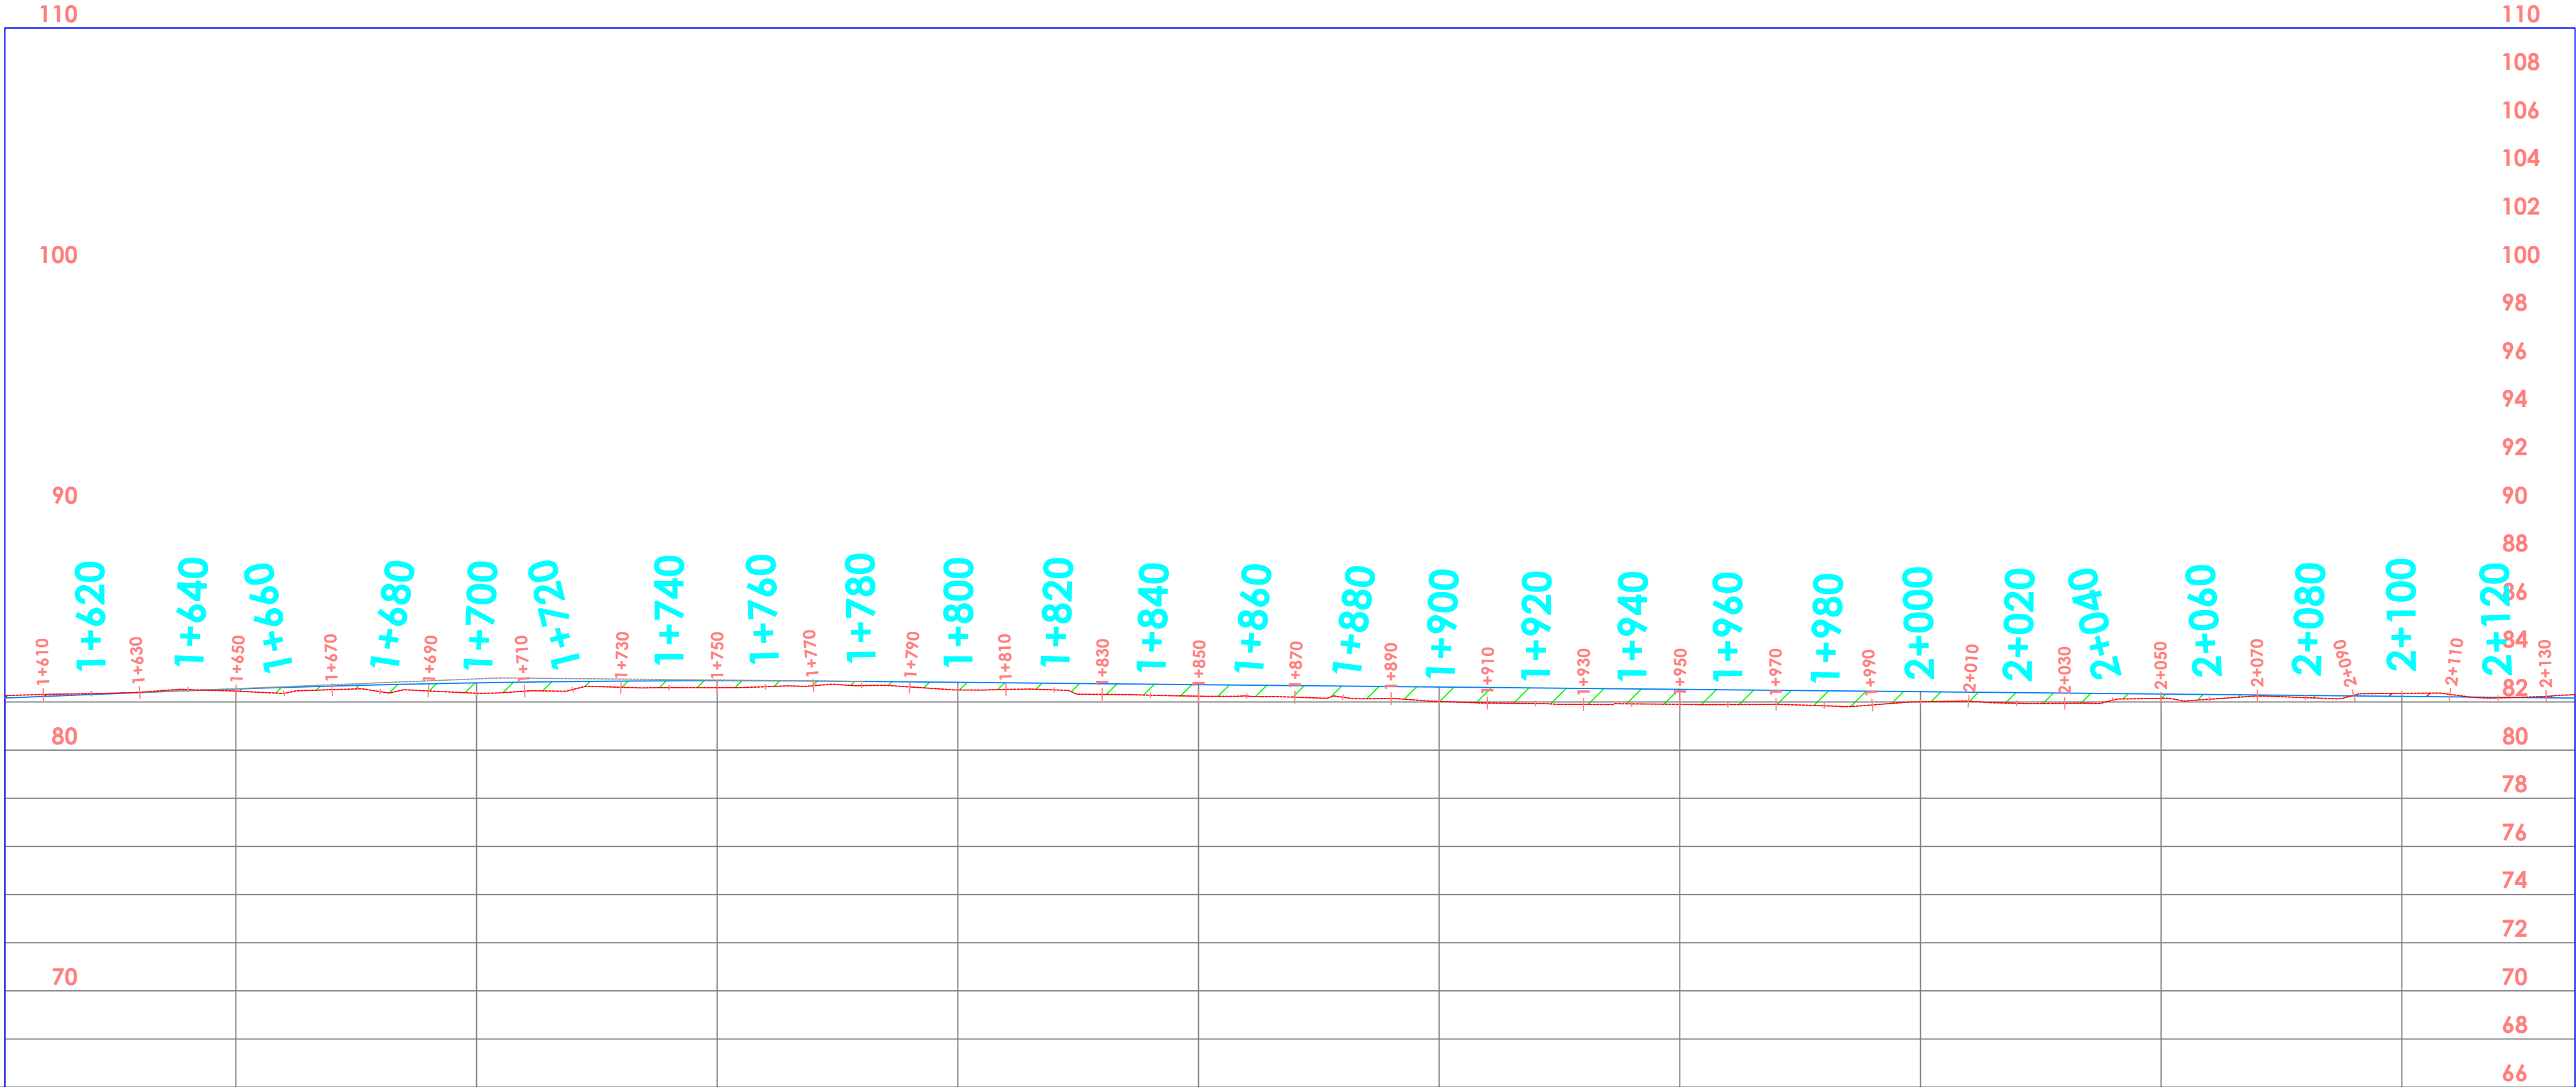

General Notes

No.	Revision/Issue	Date
-----	----------------	------

Firm Name and Address


Project Name and Address

Project
#####


Date
03.04.2025

Scale
1:1000

Sheet
4

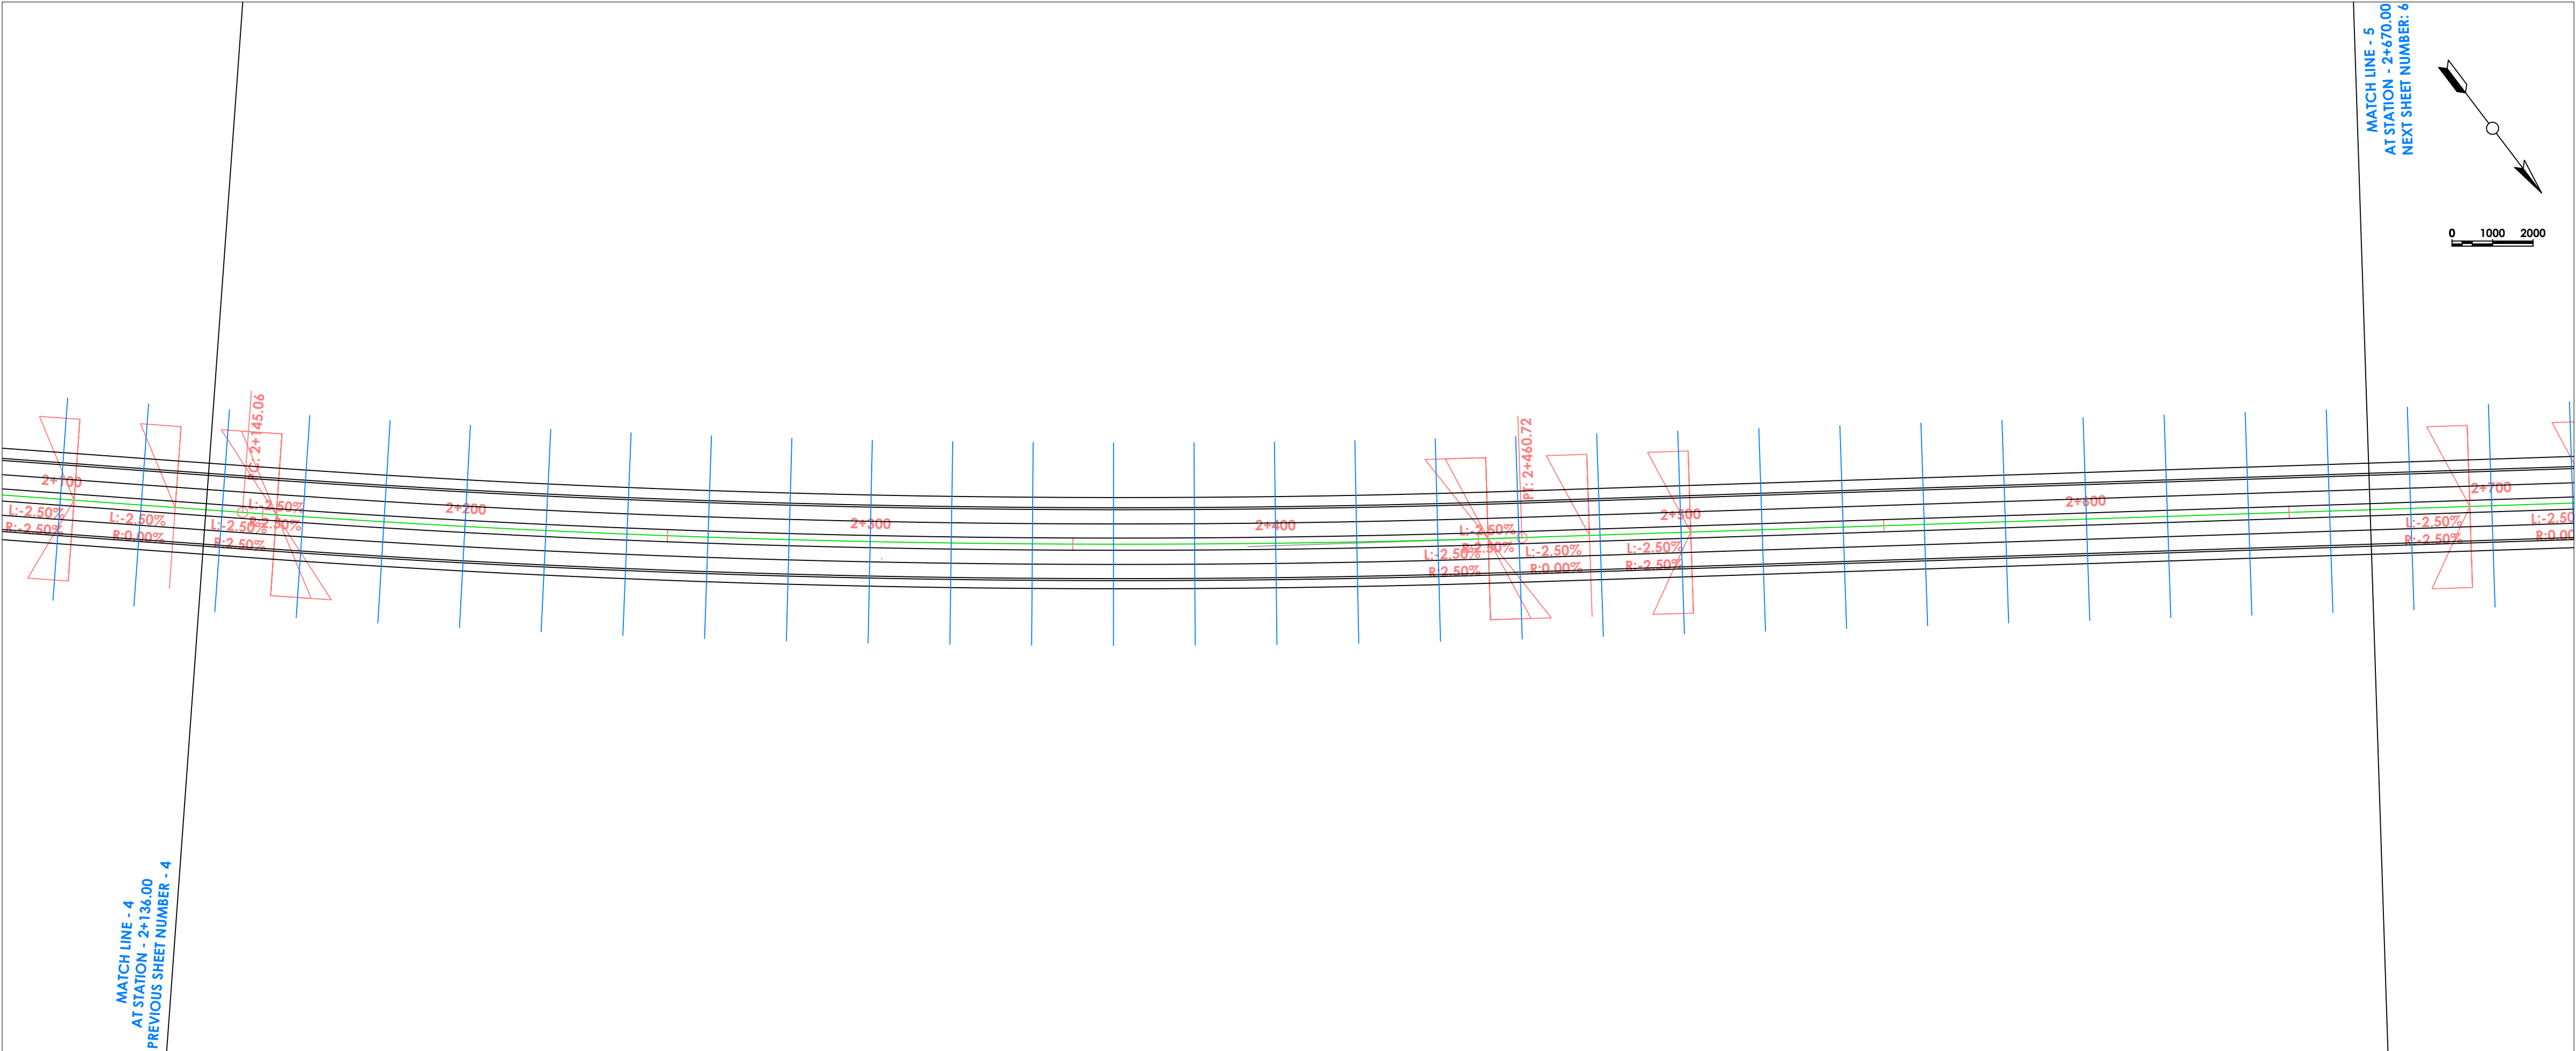

Road Design Profile

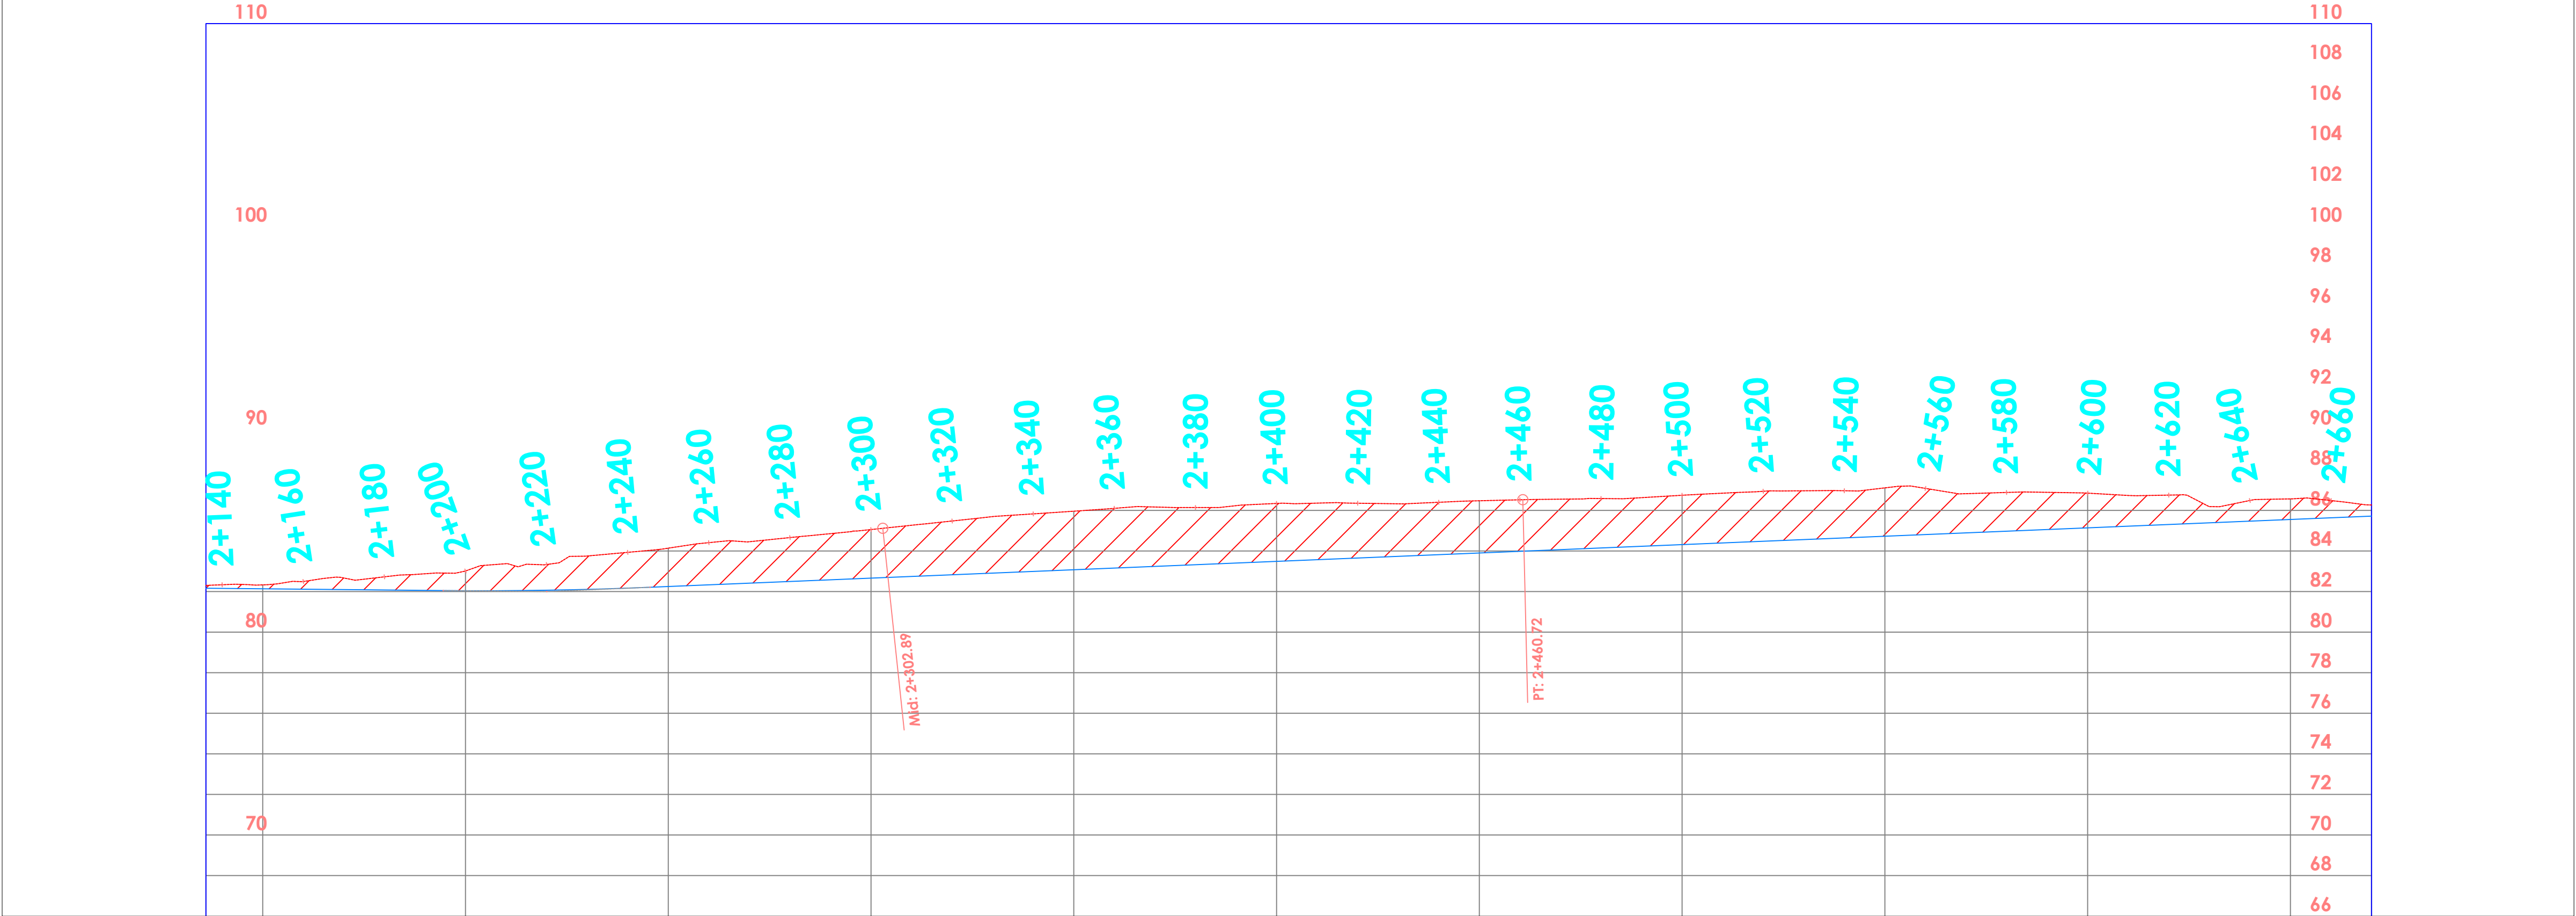

General Notes

No.	Revision/Issue	Date
-----	----------------	------

Firm Name and Address

Project Name and Address

#####


Project#####

Date03.04.2025


Scale1:1000

Sheet

5

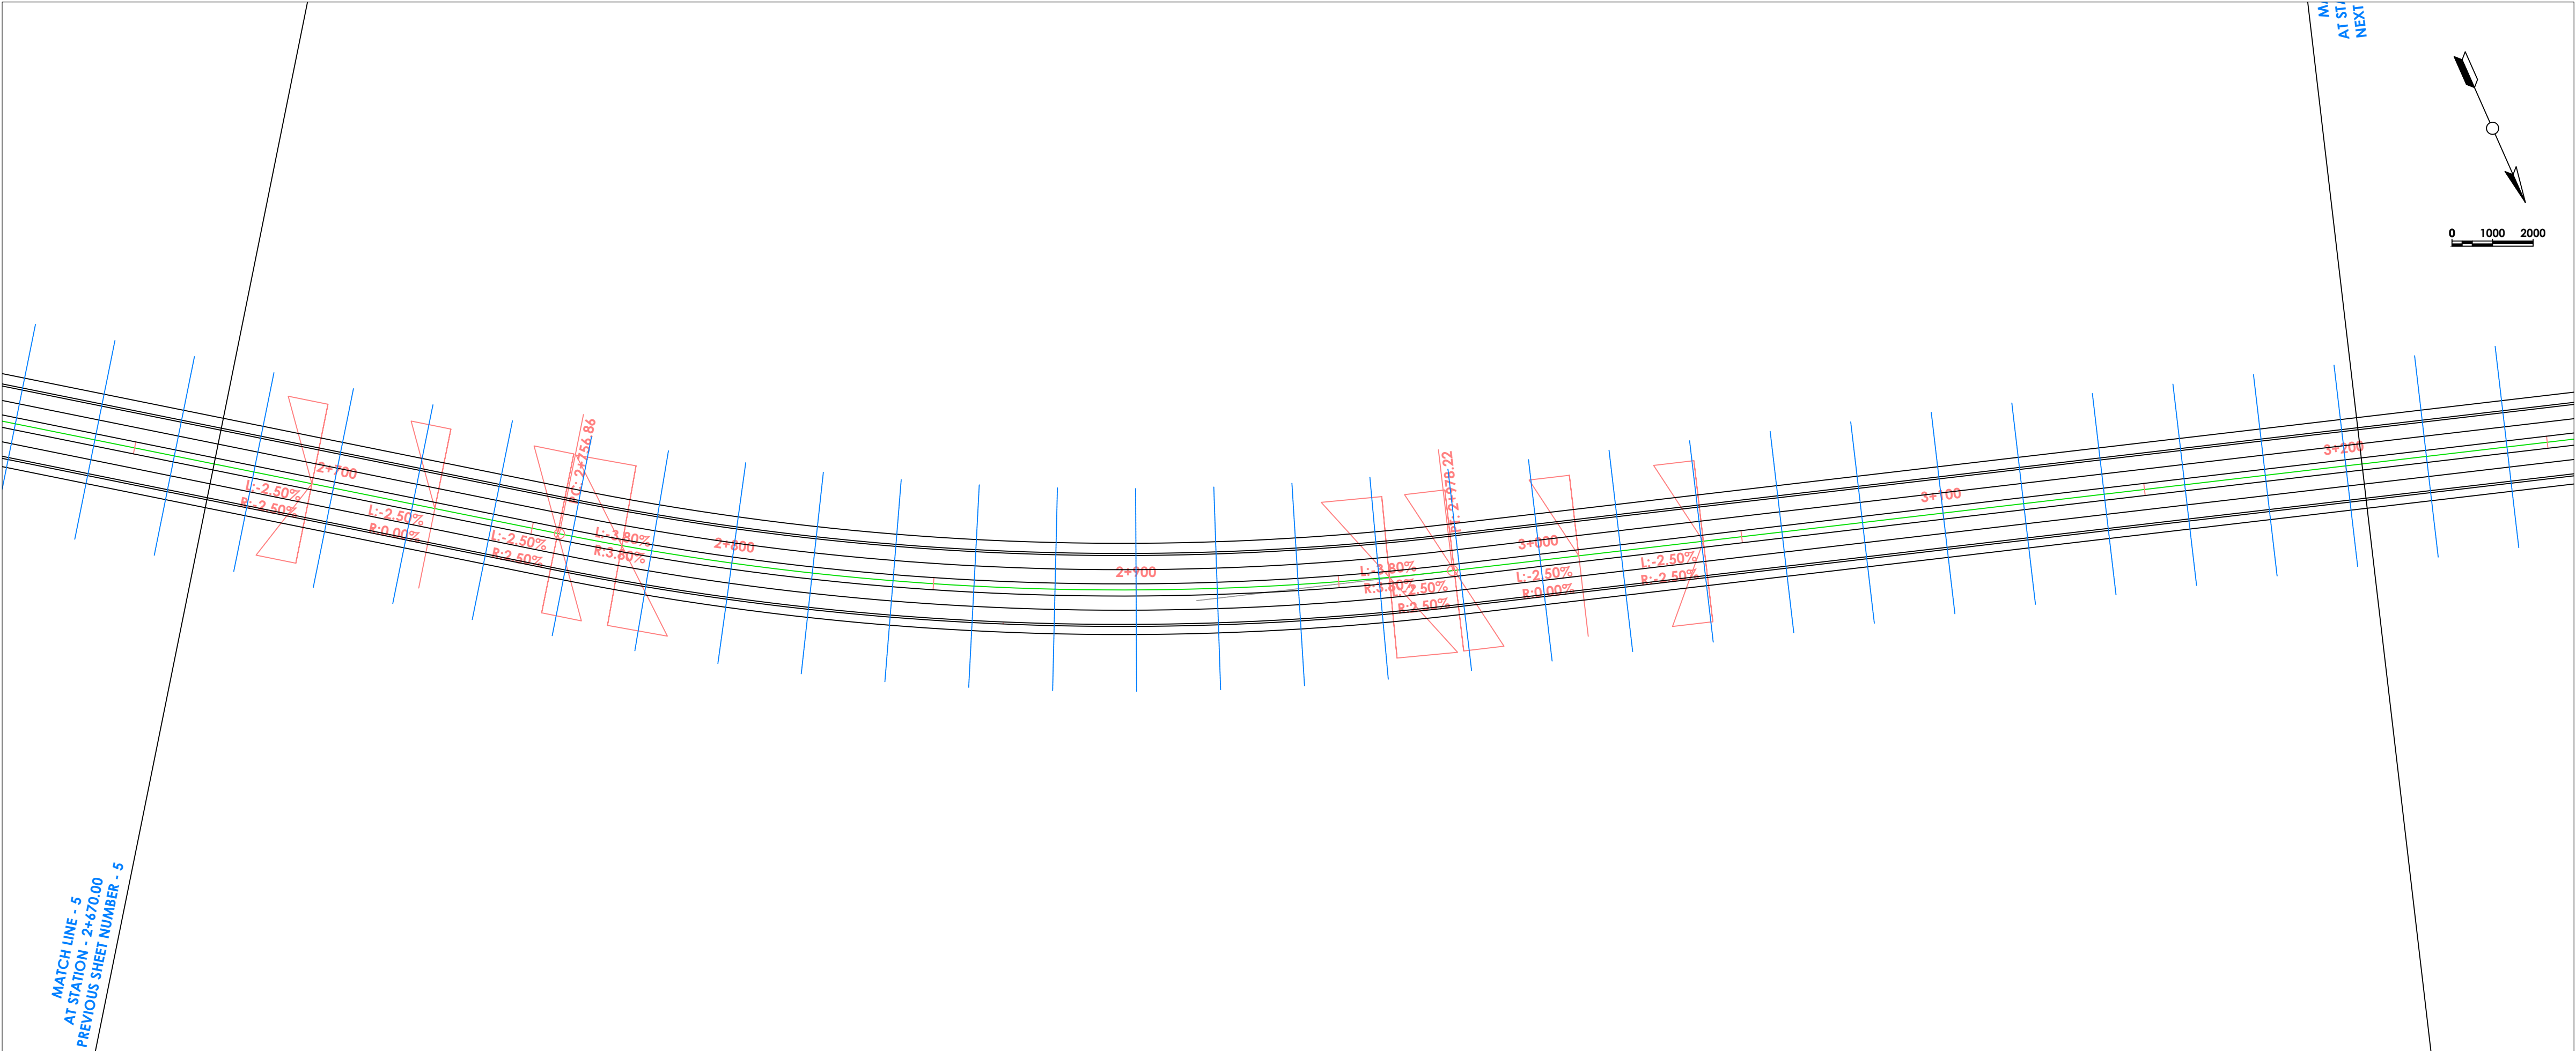

Road Design Profile

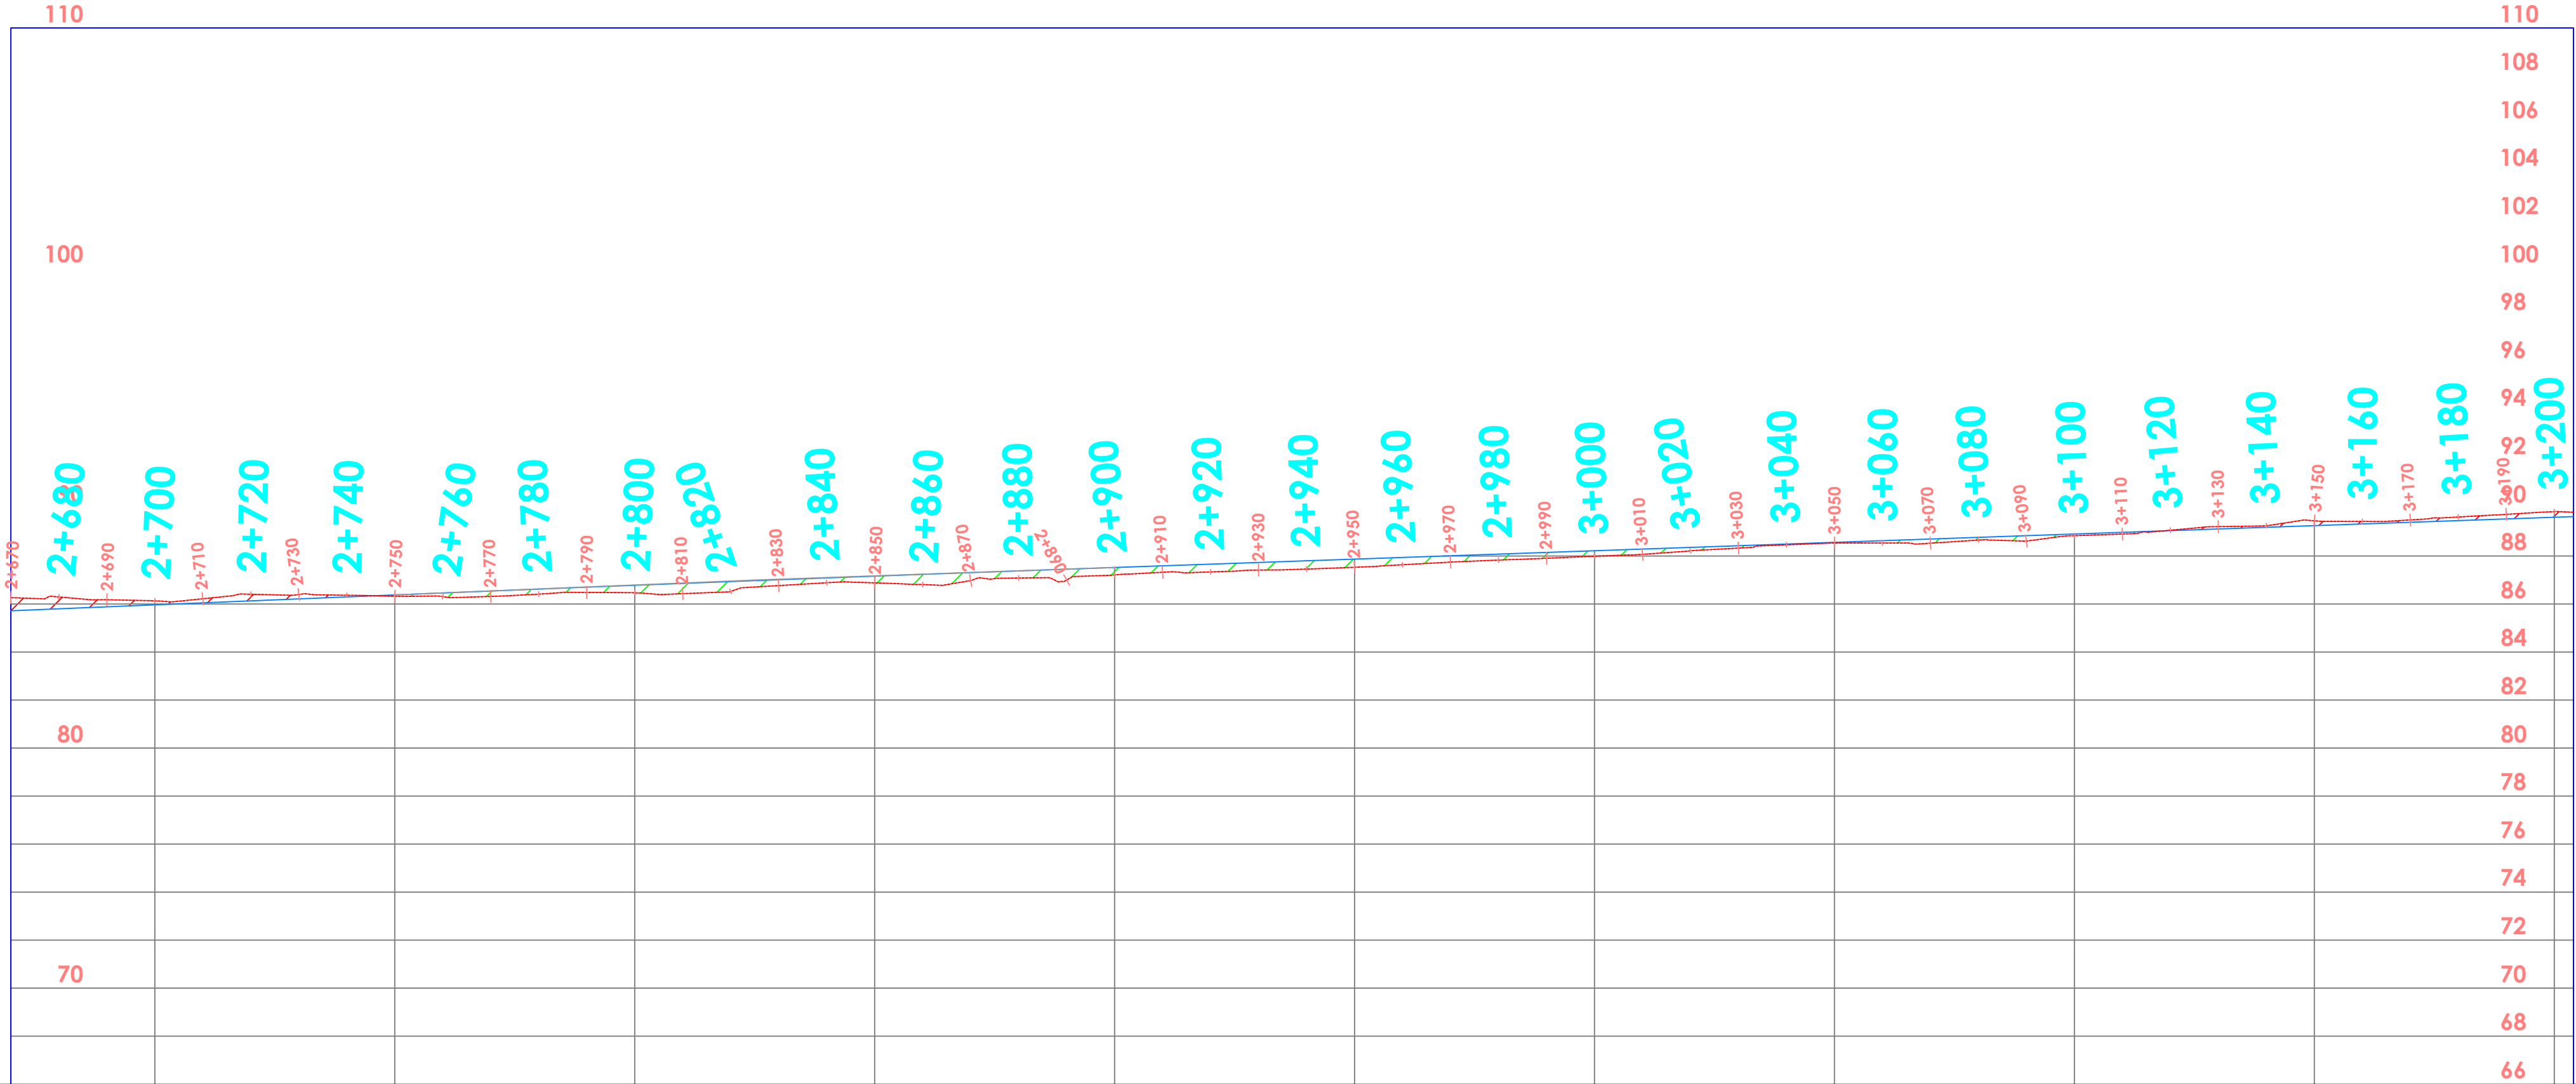

General Notes


No.	Revision/Issue	Date

Firm Name and Address


Project Name and Address

#####

Project	#####	Sheet	6
Date	03.04.2025		
Scale	1:1000		

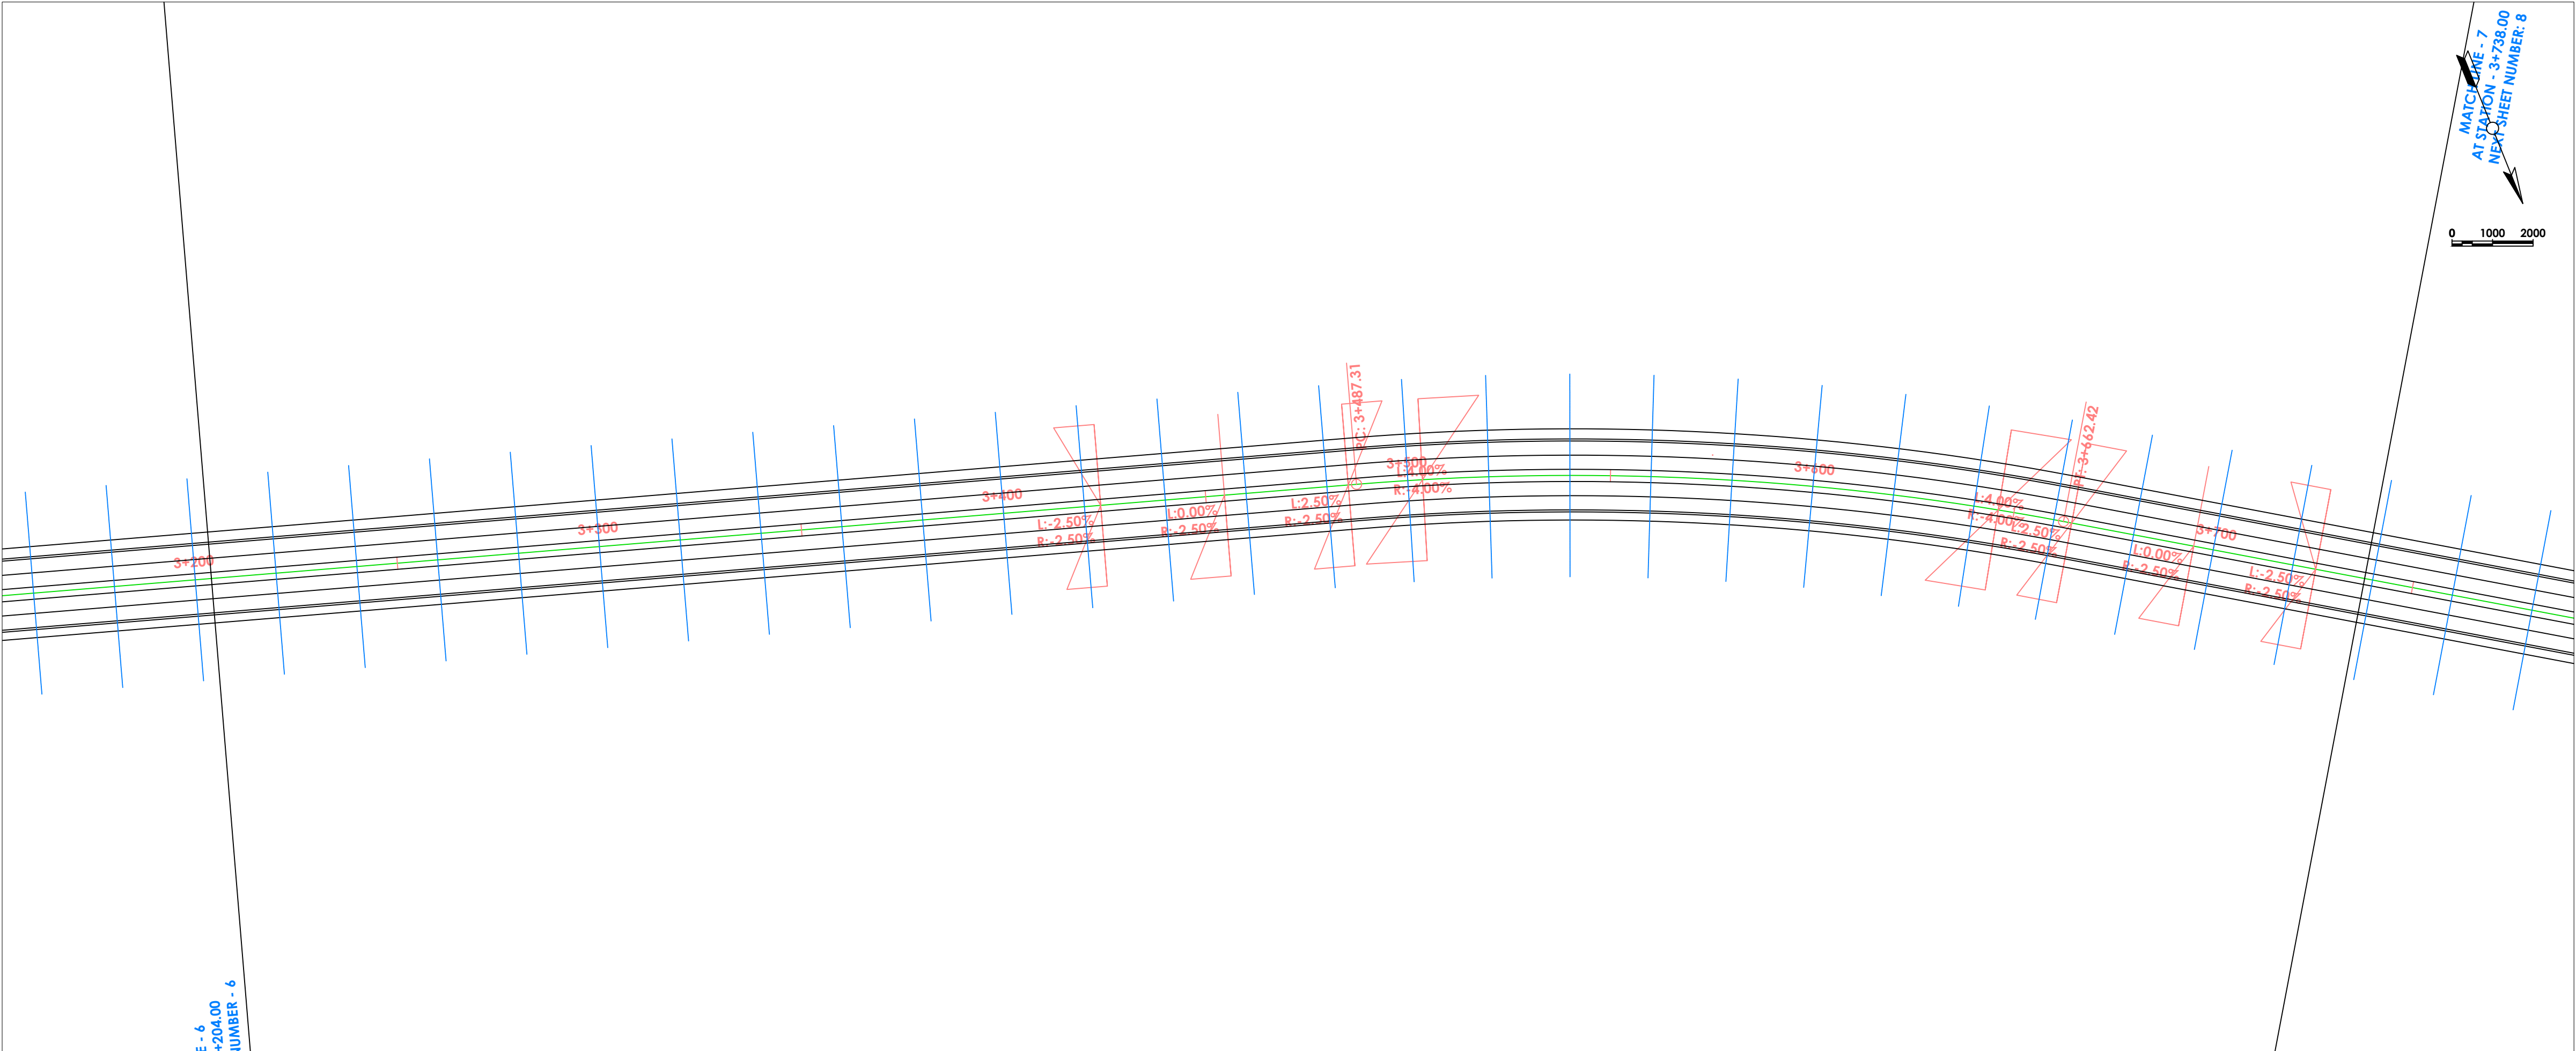

Road Design Profile

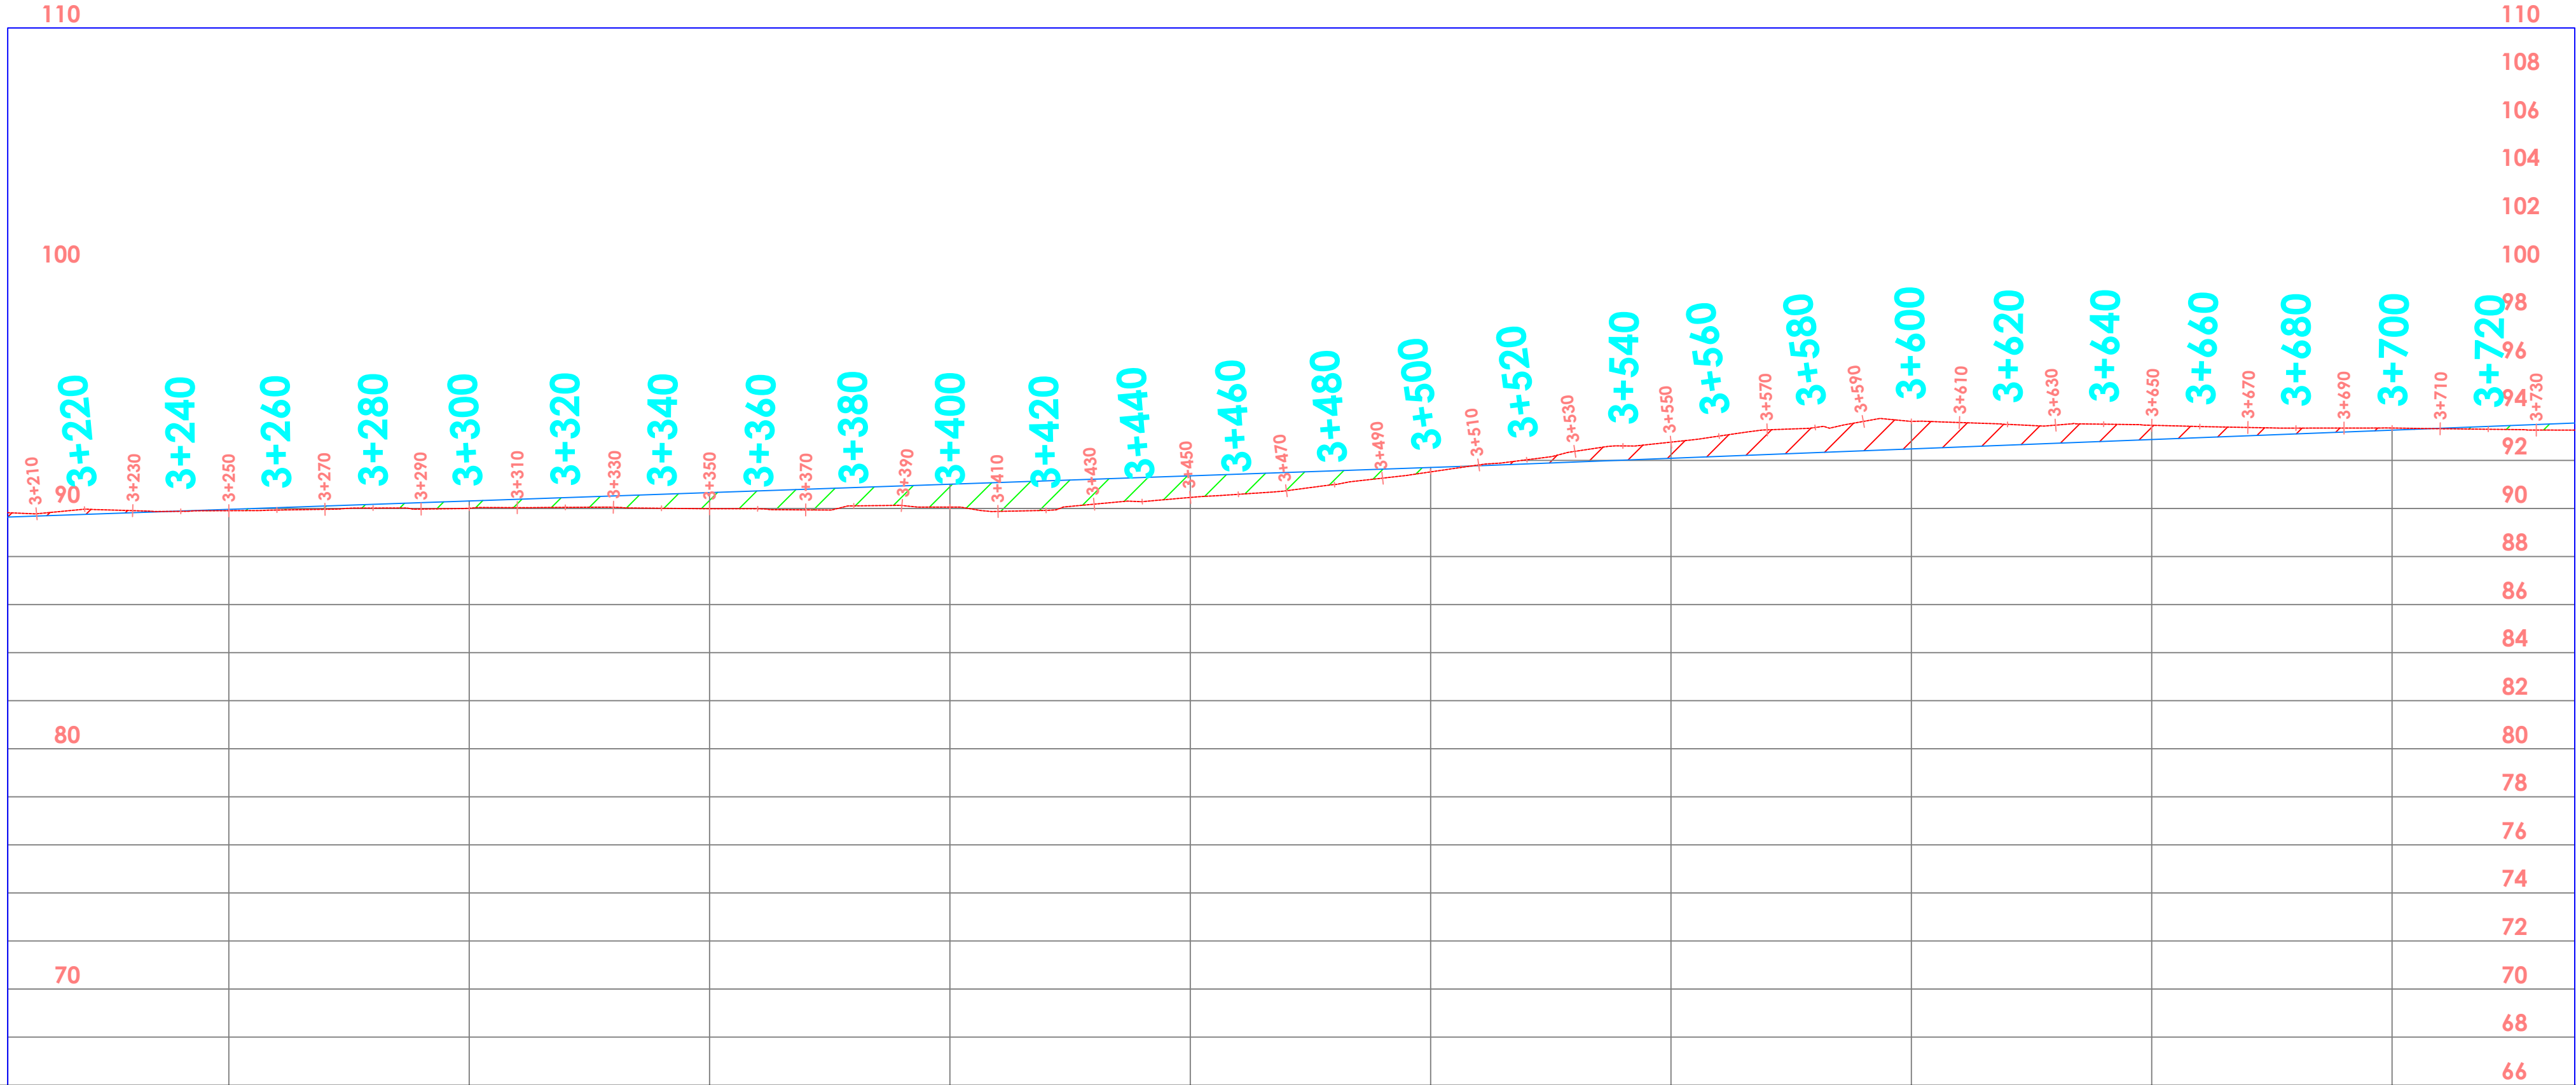

General Notes

No.	Revision/Issue	Date
-----	----------------	------

Firm Name and Address


Project Name and Address

Project
#####


Date
03.04.2025

Scale
1:1000

Sheet
7

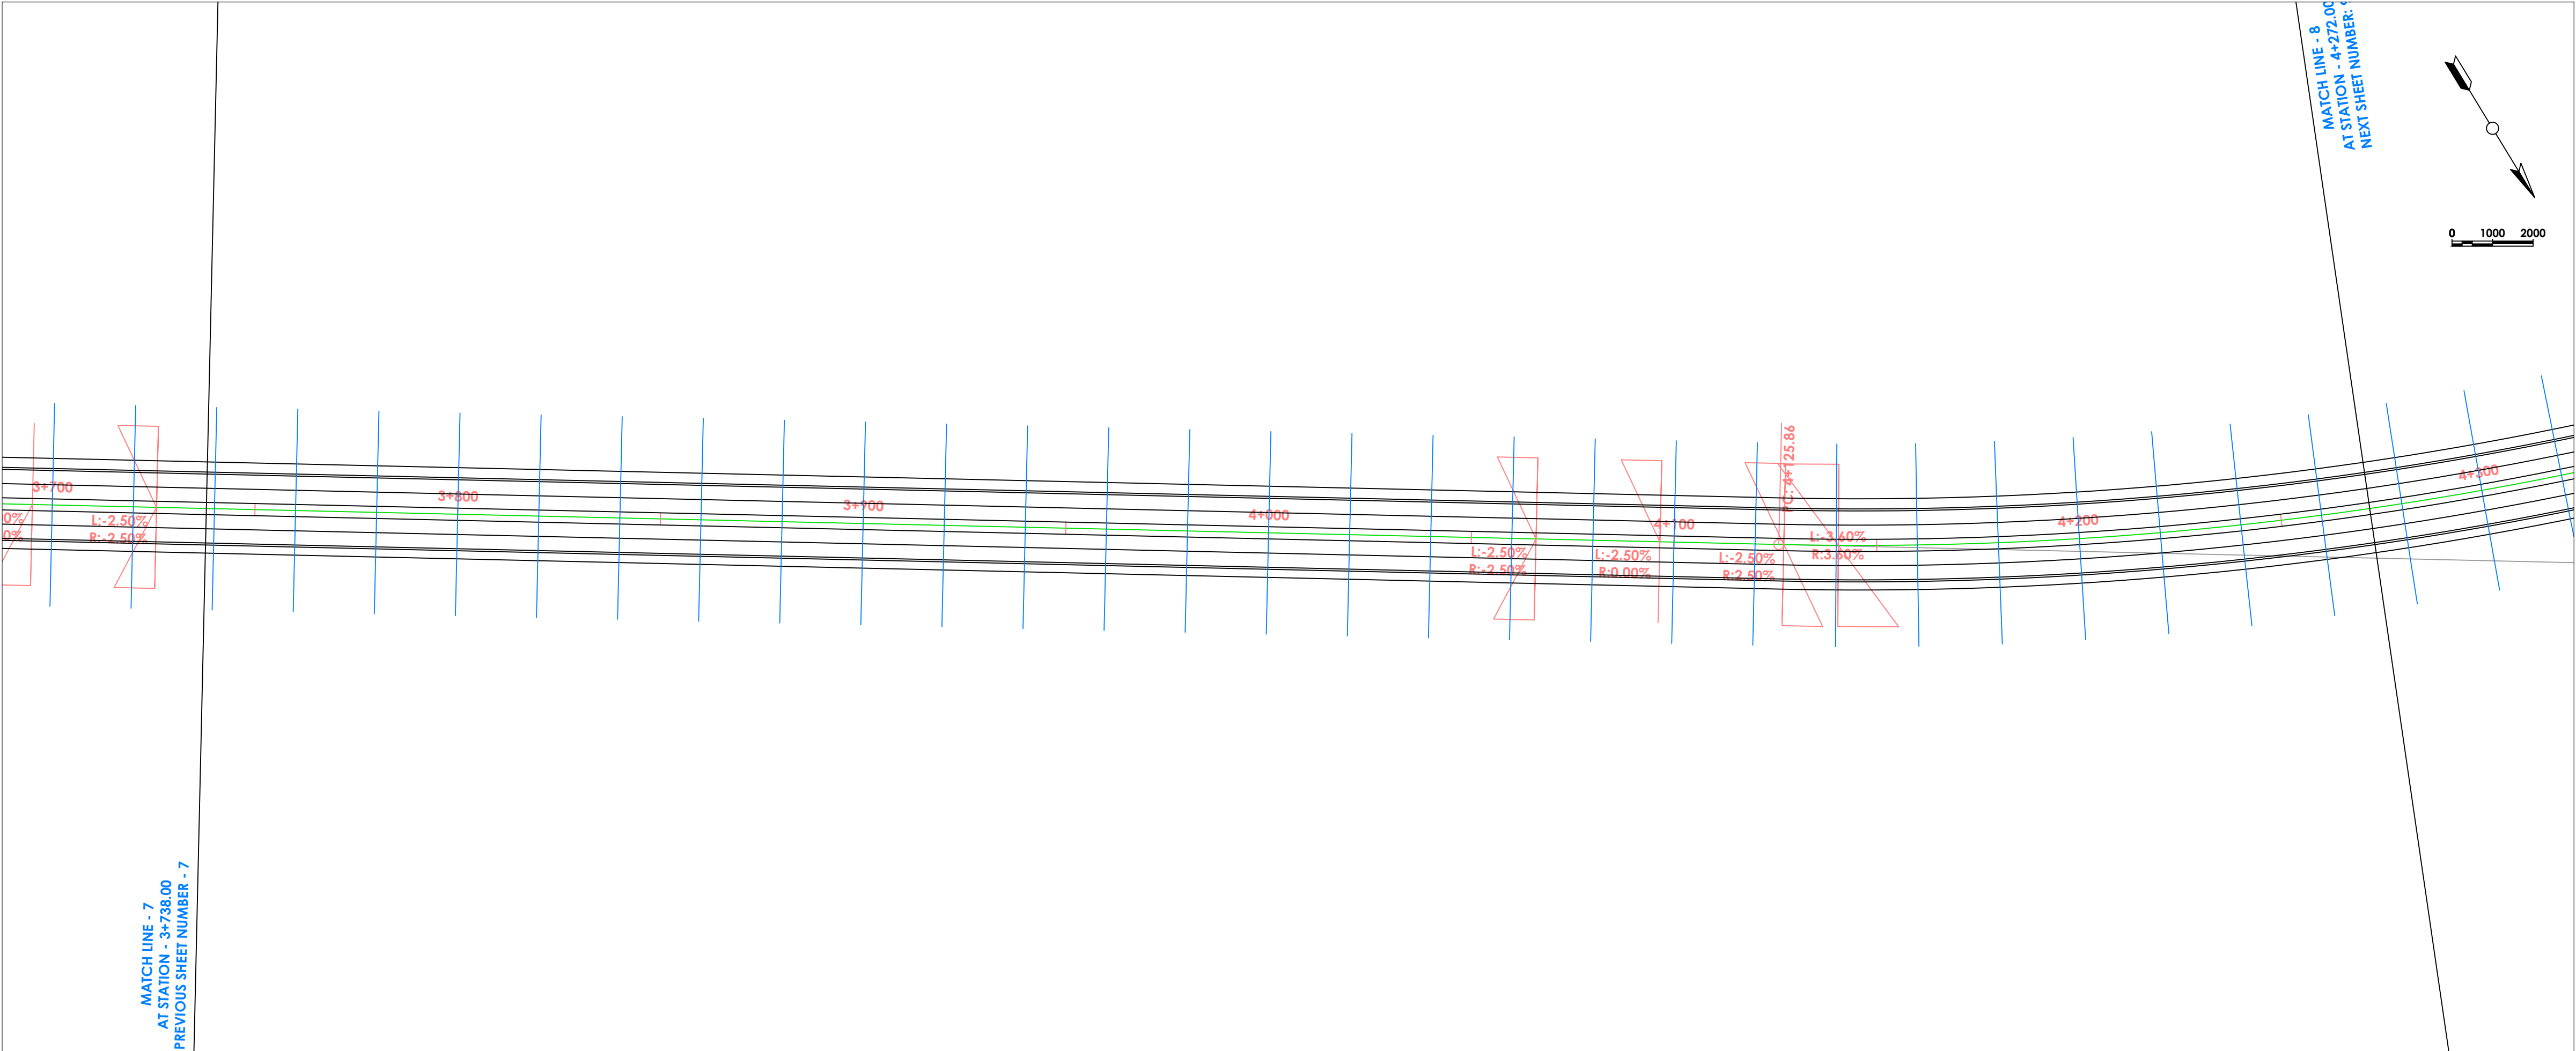

Road Design Profile

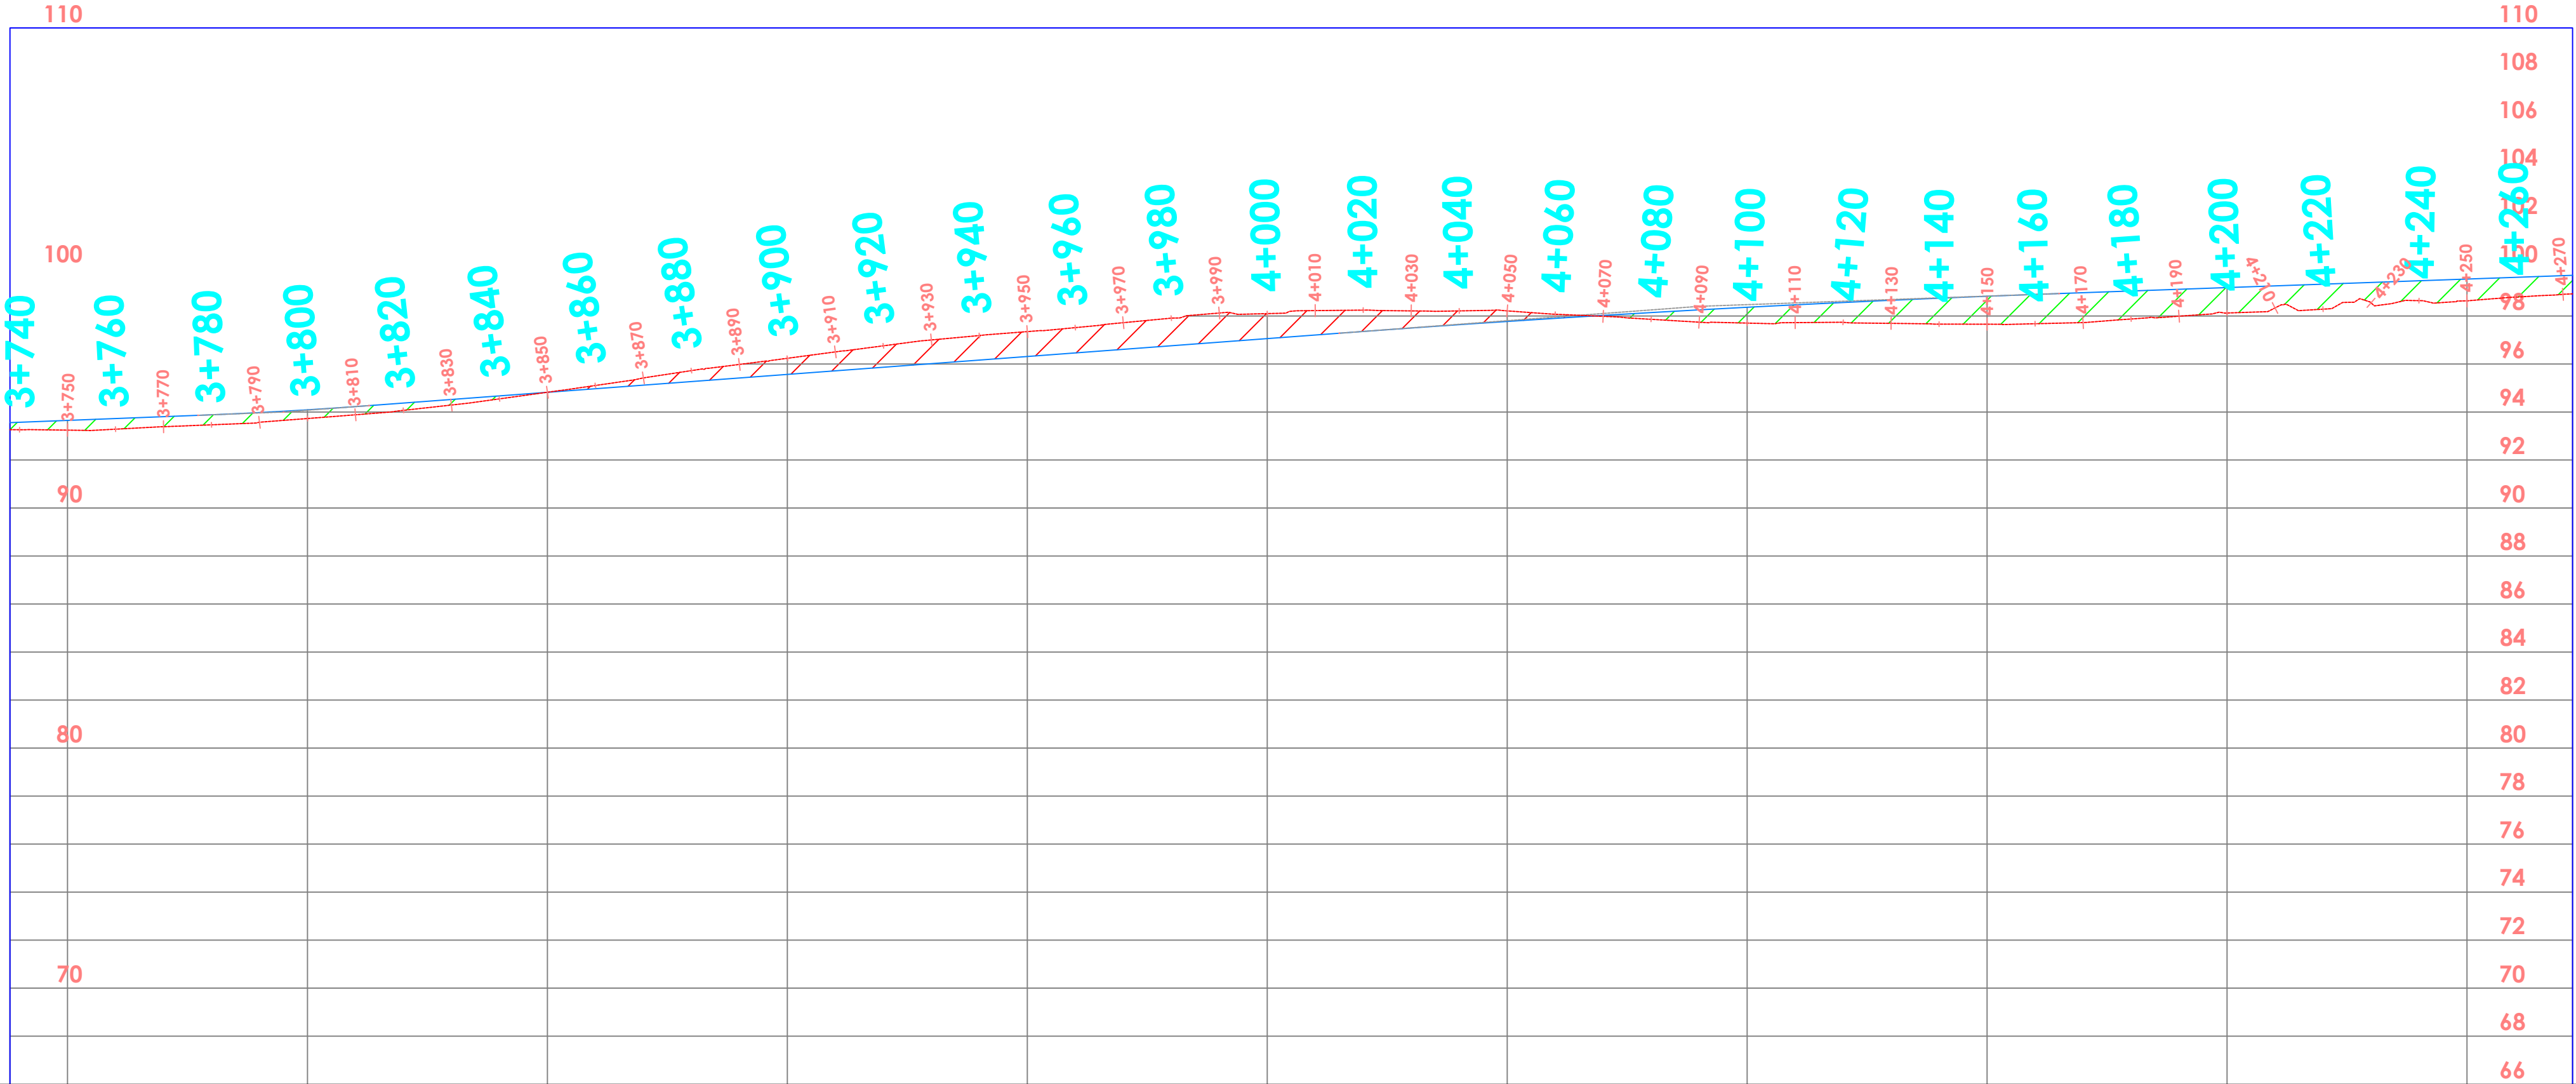

General Notes

No.	Revision/Issue	Date
-----	----------------	------

Firm Name and Address


Project Name and Address

Project
#####


Date
03.04.2025

Scale
1:1000

Sheet
8

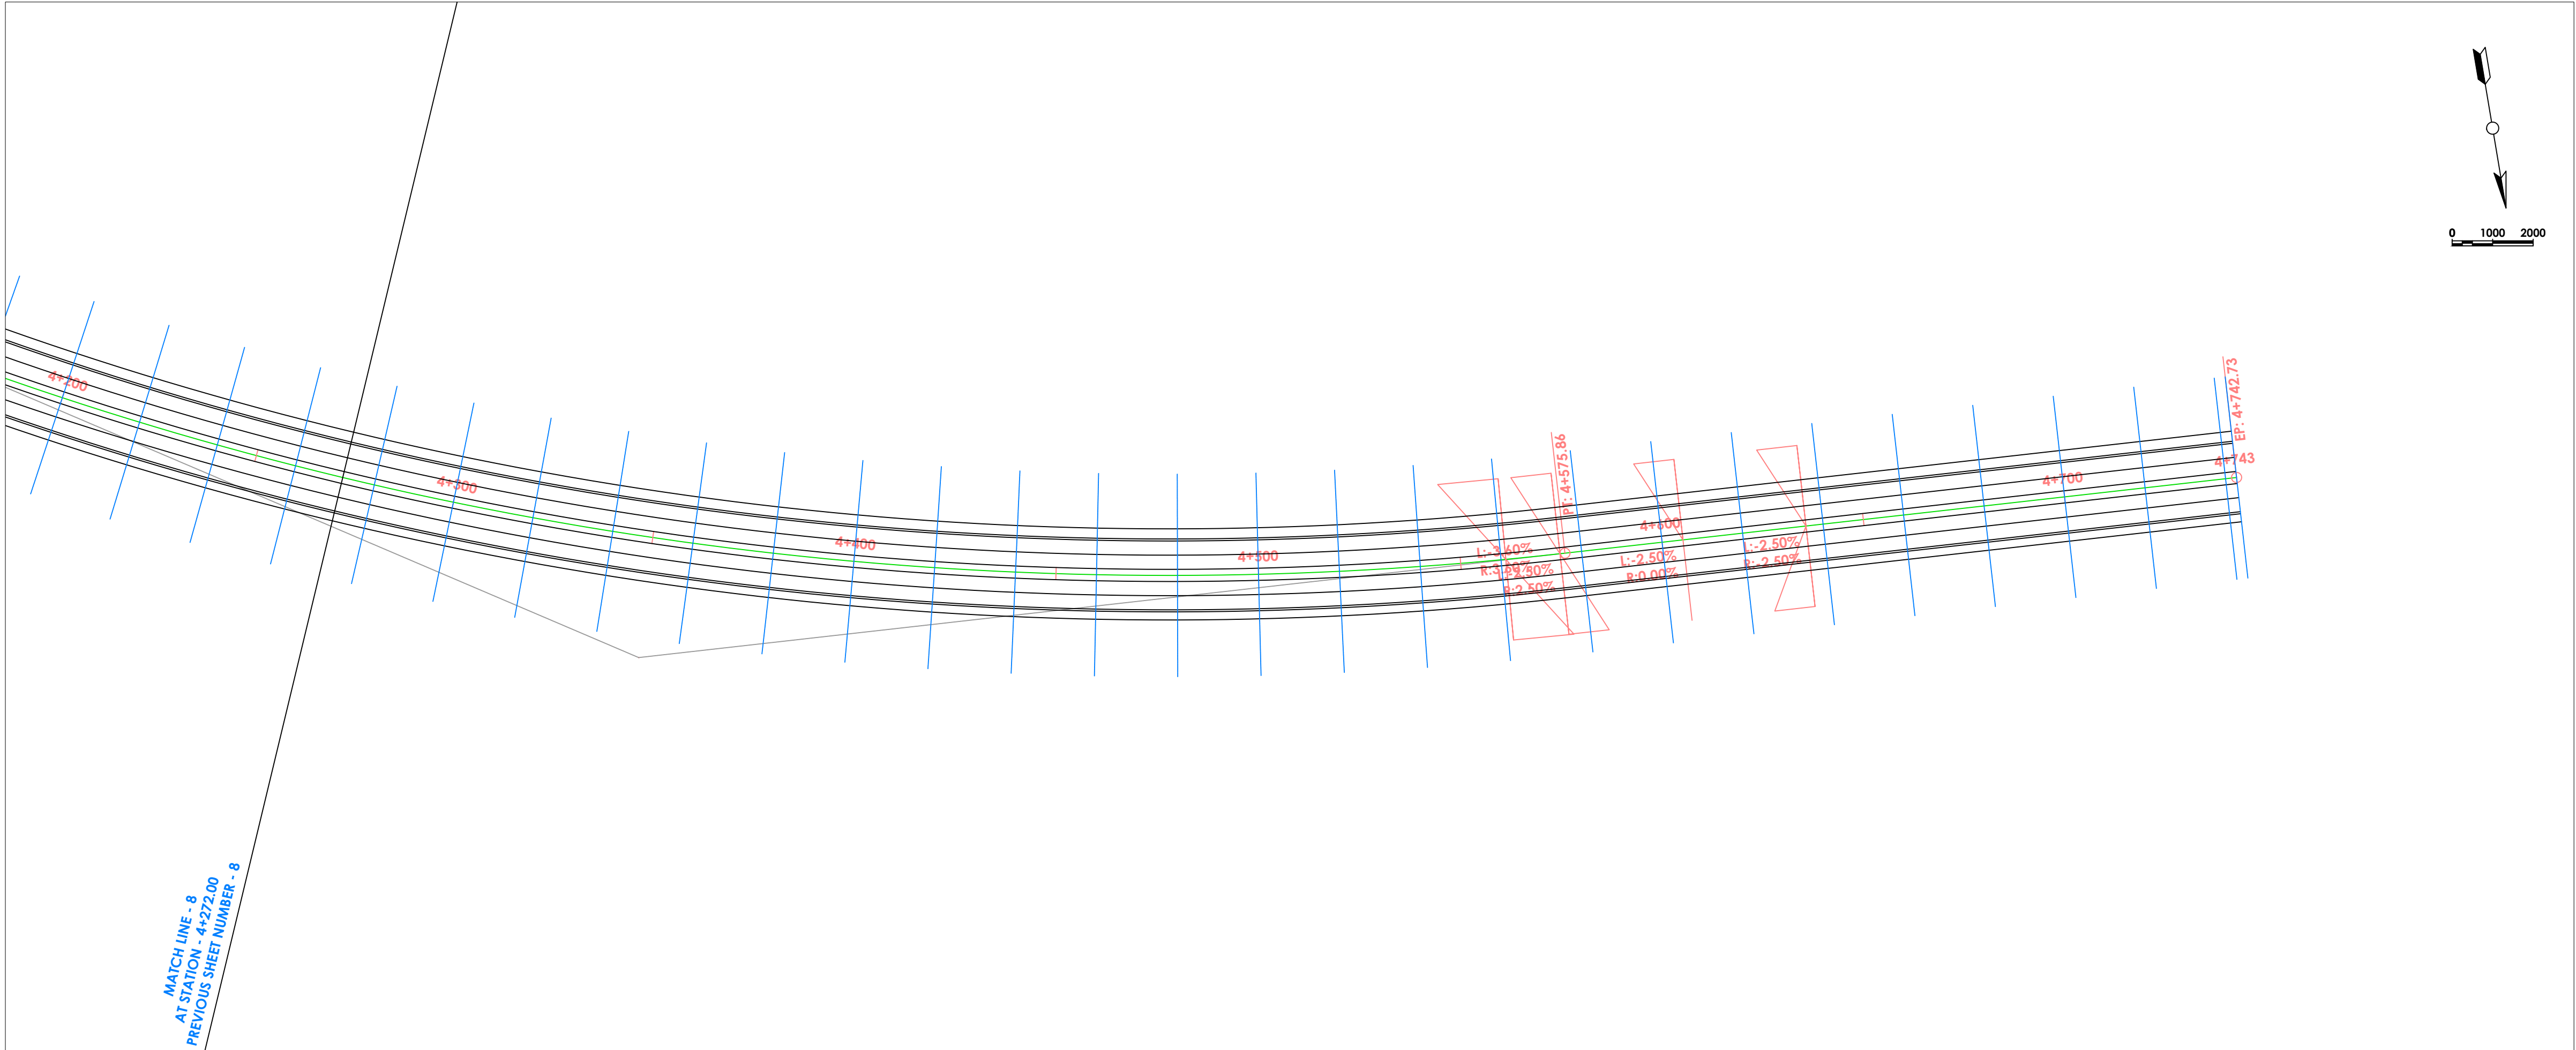

Road Design Profile

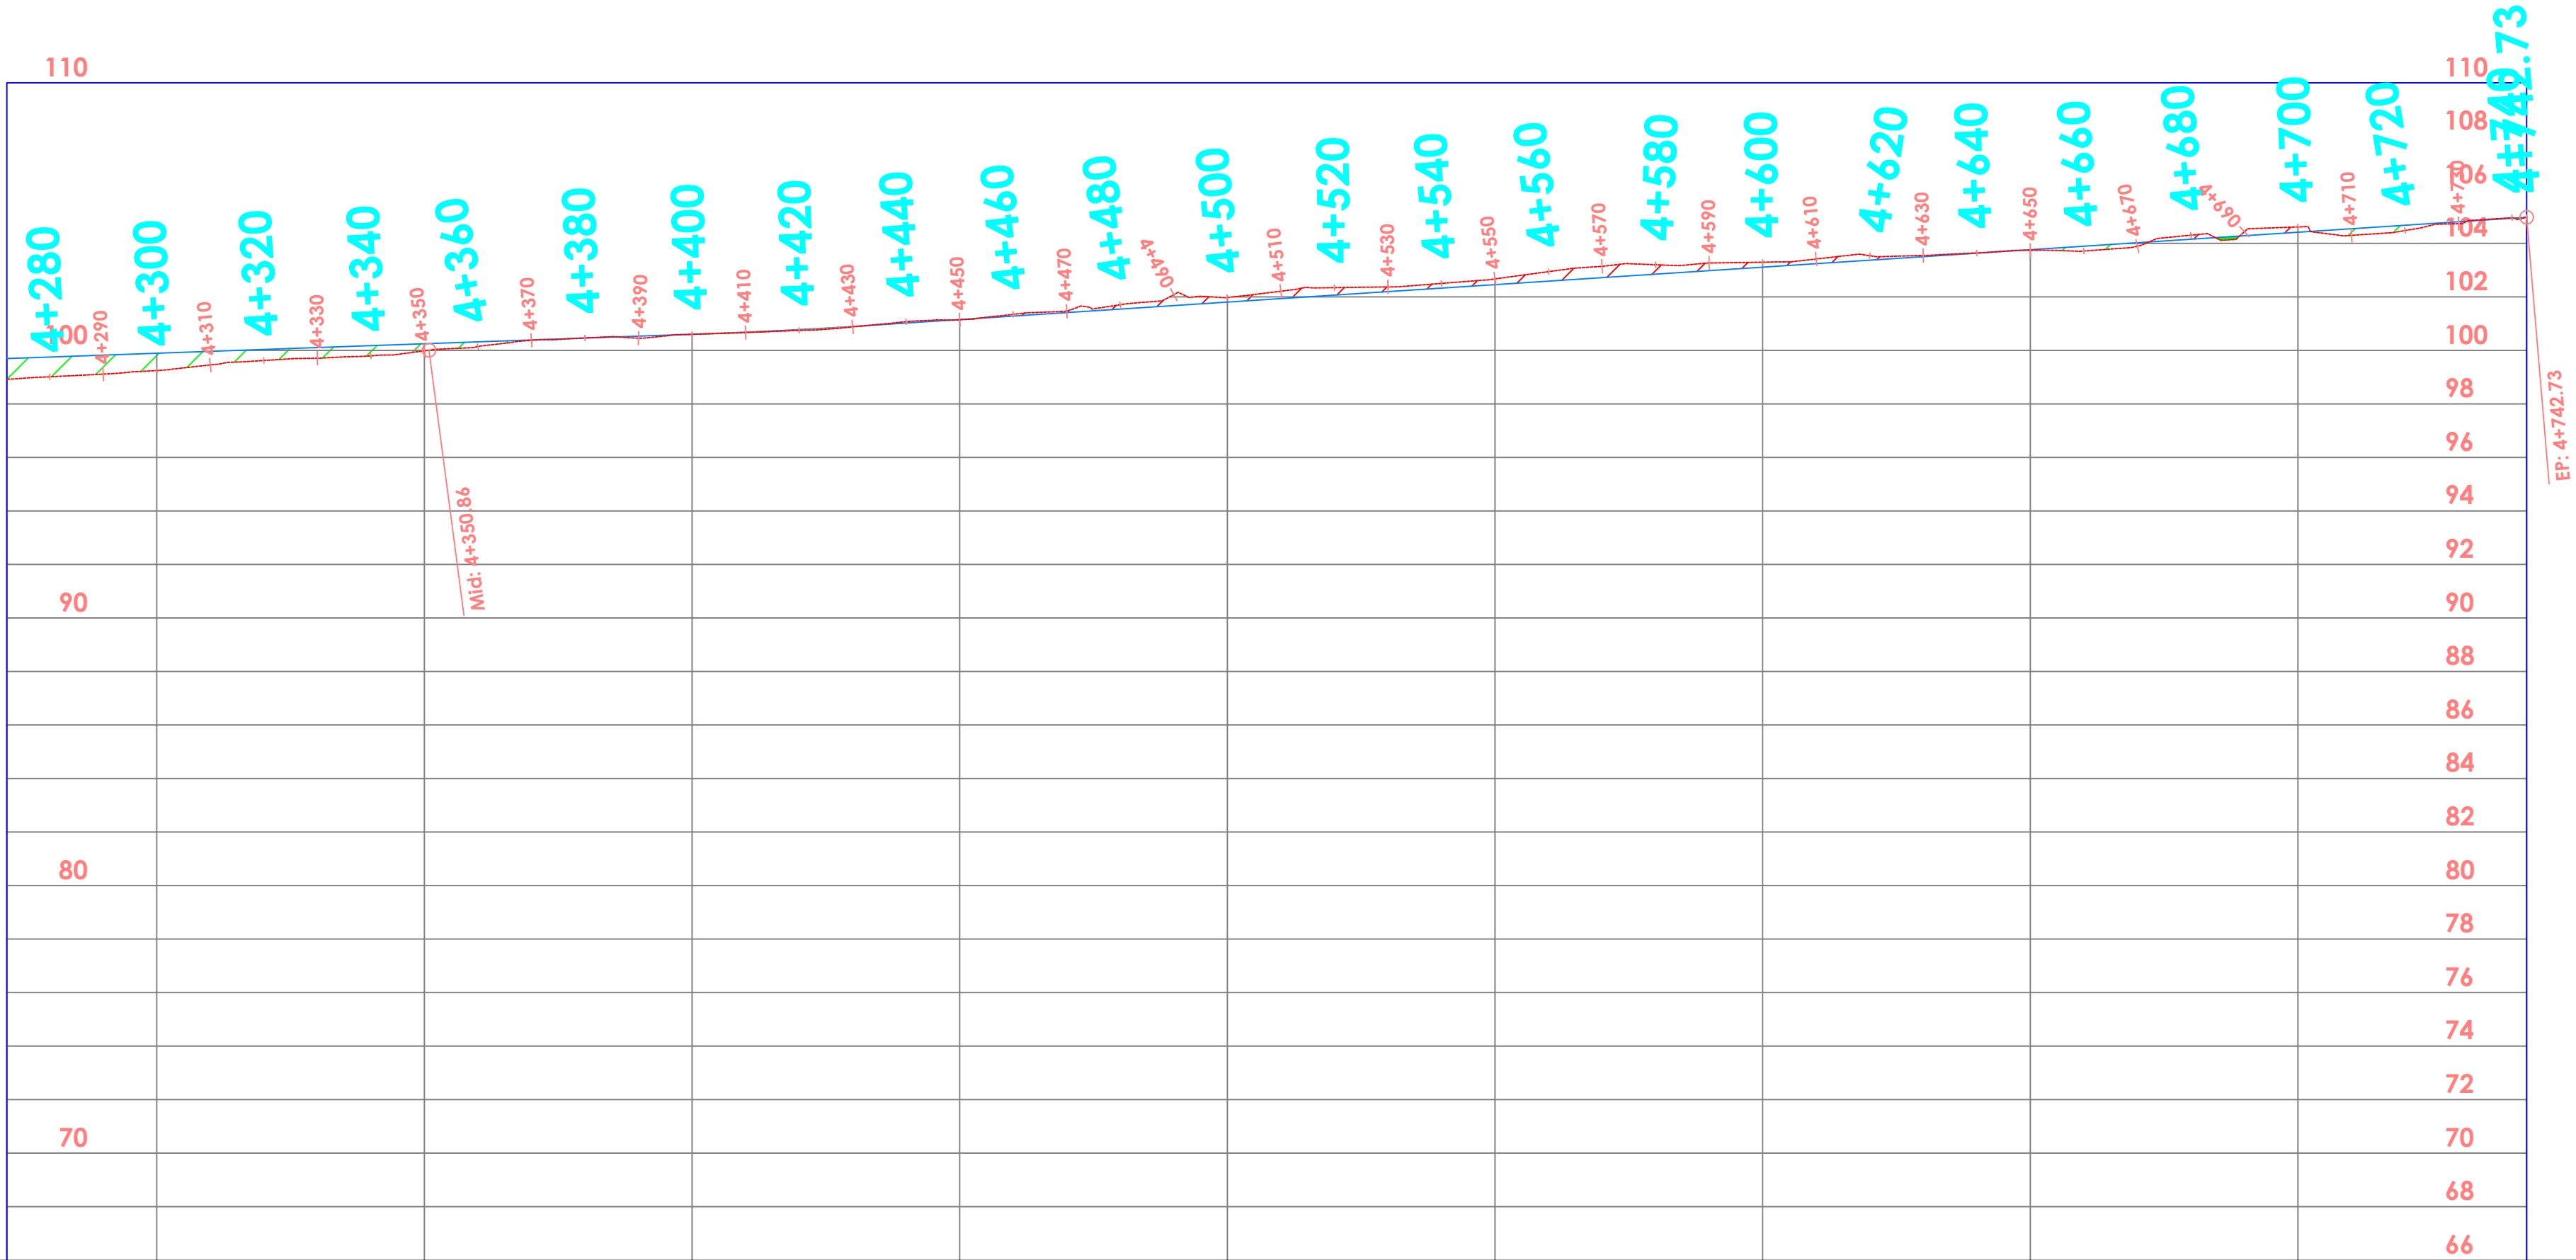

General Notes

No.	Revision/Issue	Date

Firm Name and Address

Project Name and Address

#####

Project	#####	Sheet 9
Date	03.04.2025	
Scale	1:1000	